




FONDATIONS

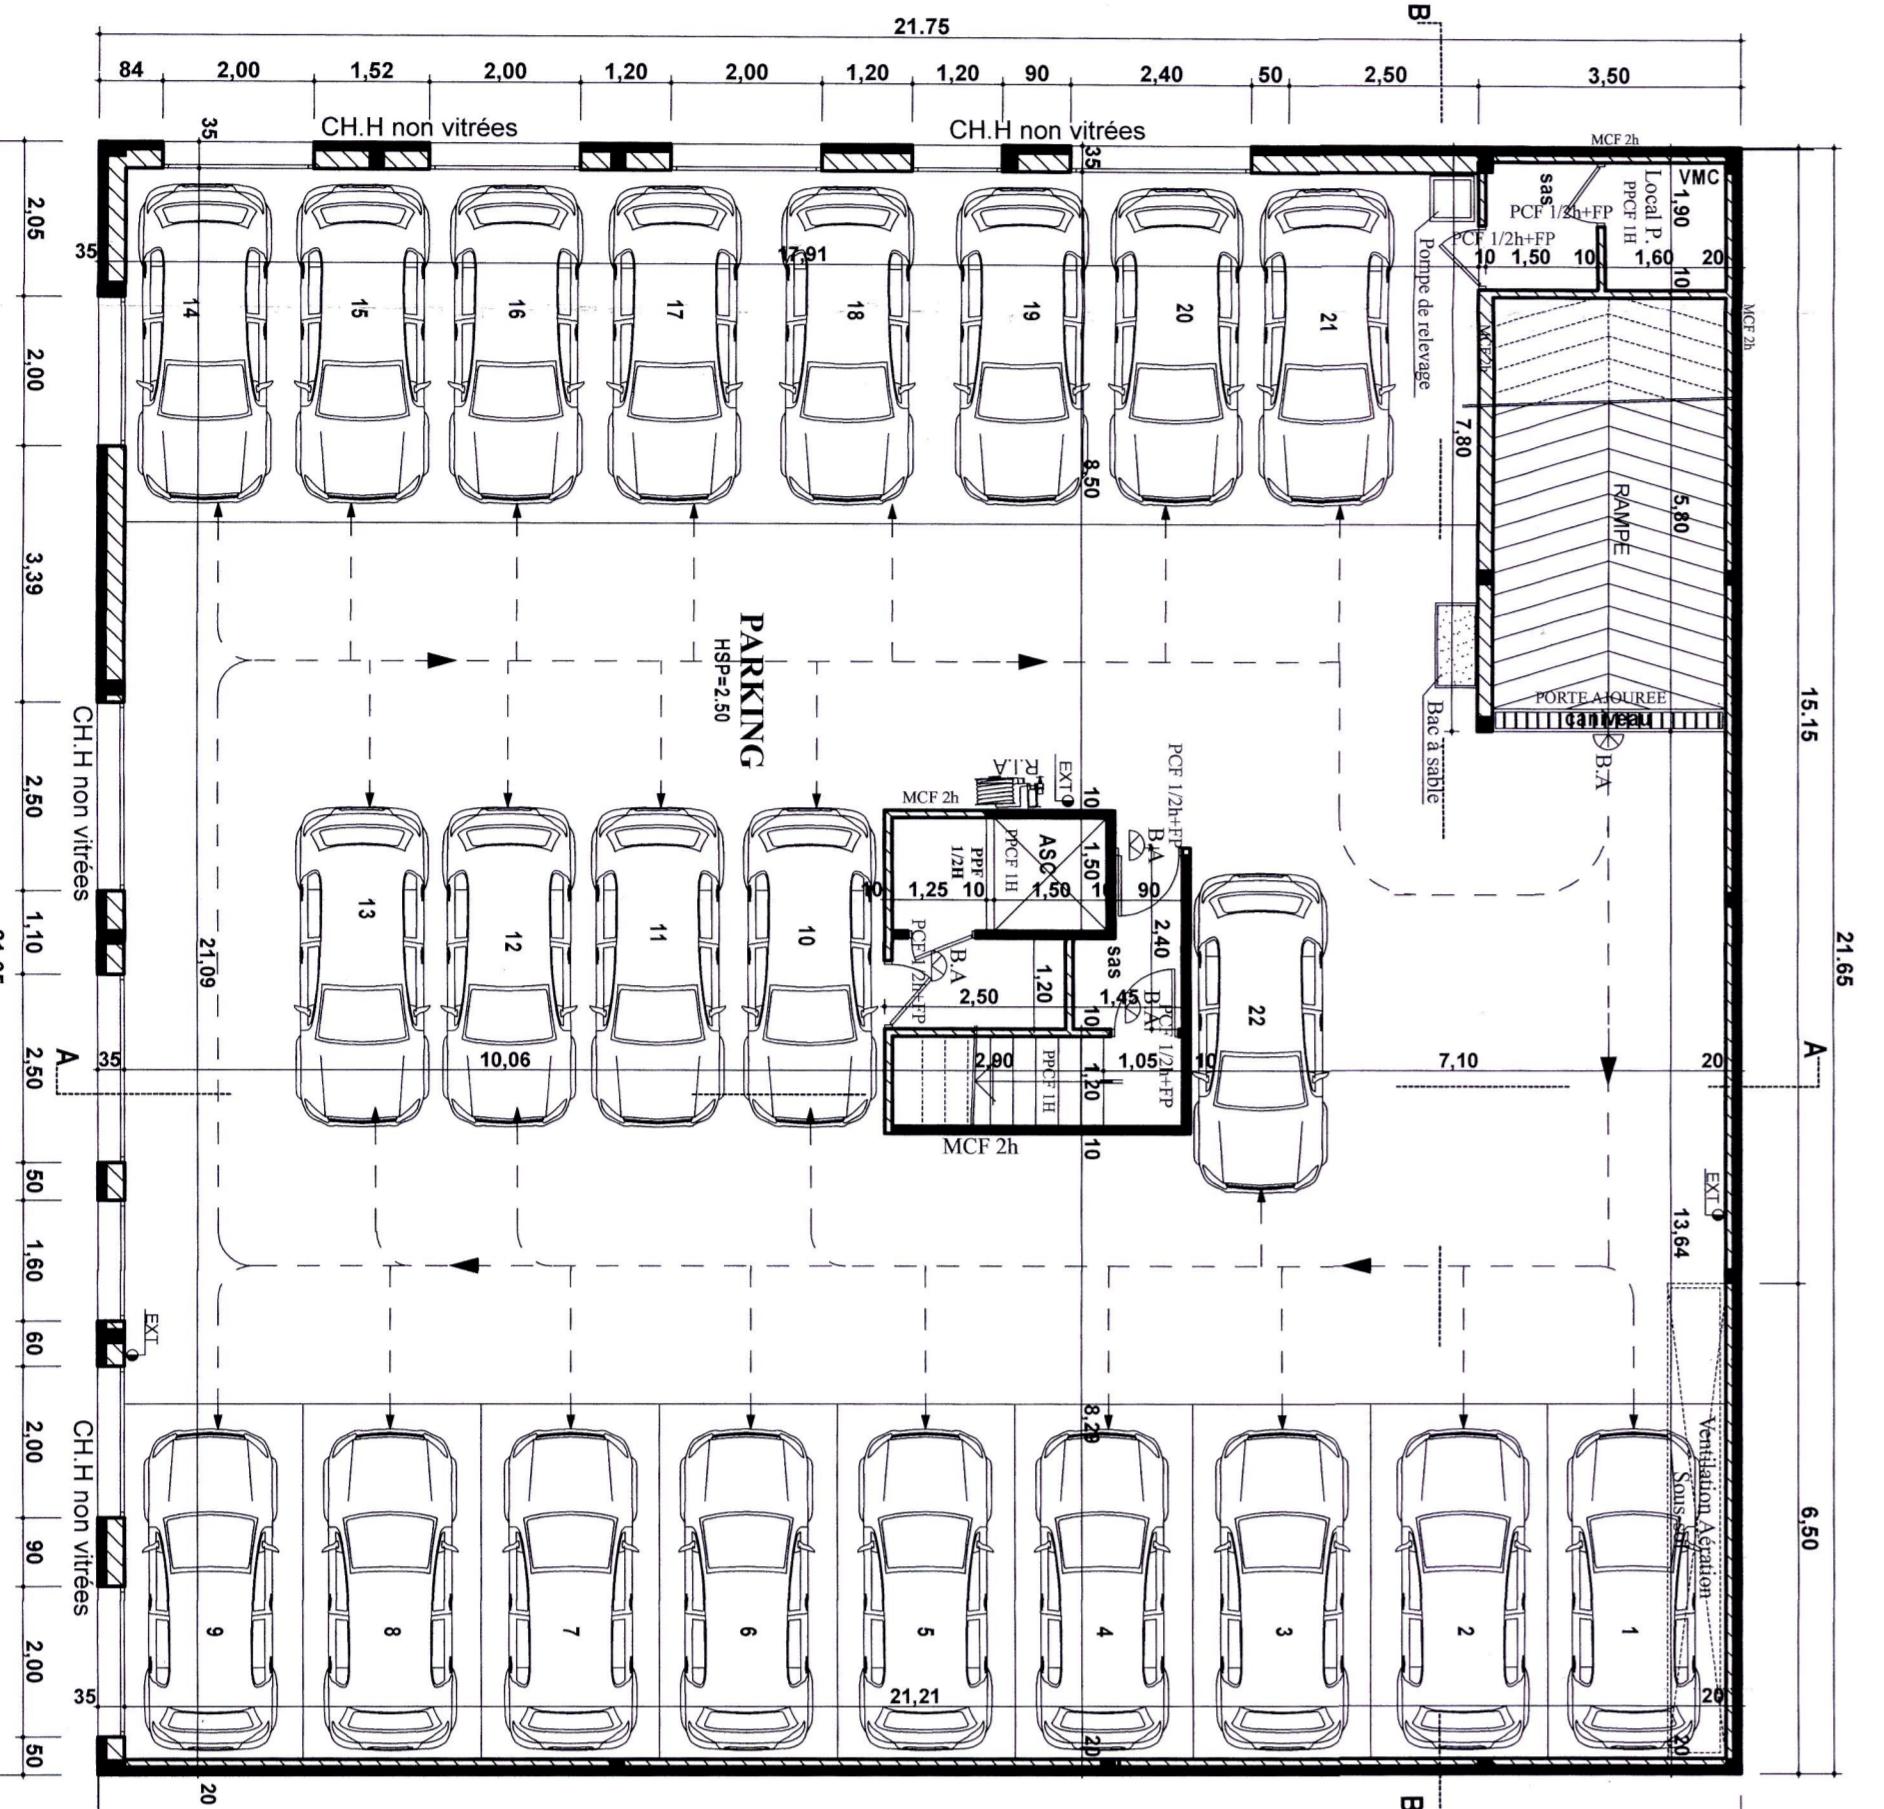


PLAN SOUS SOL

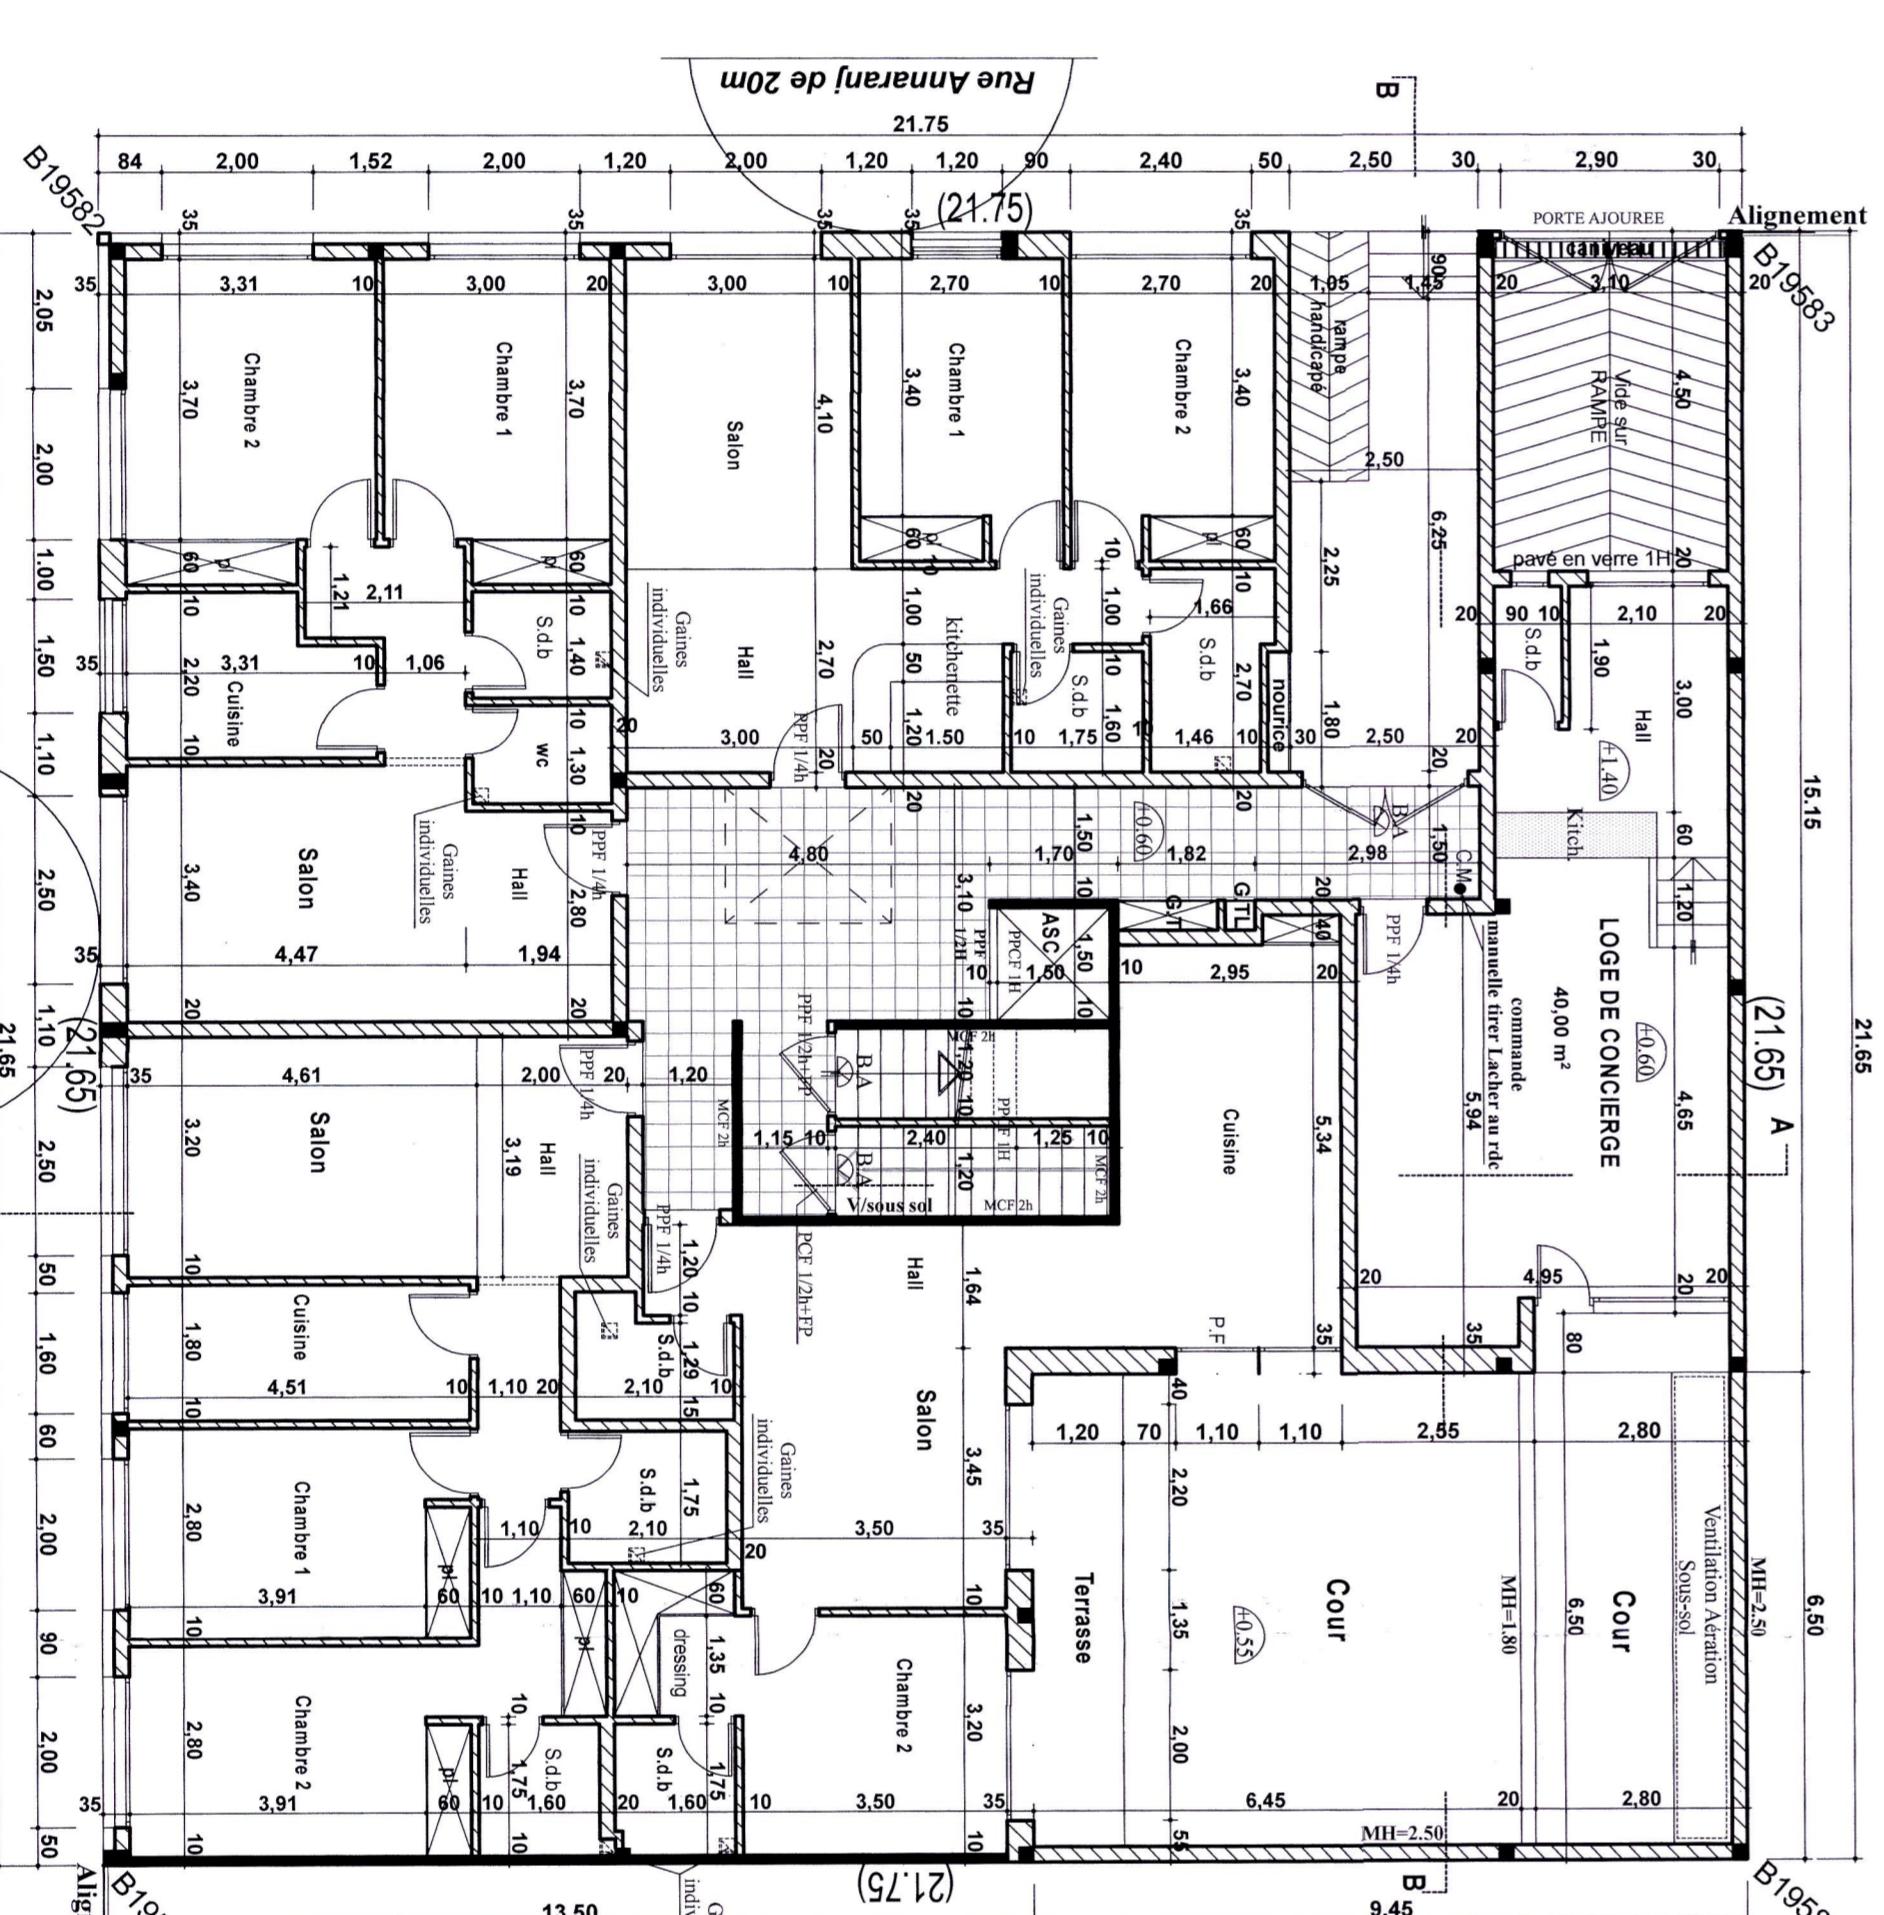

PLAN RDCH

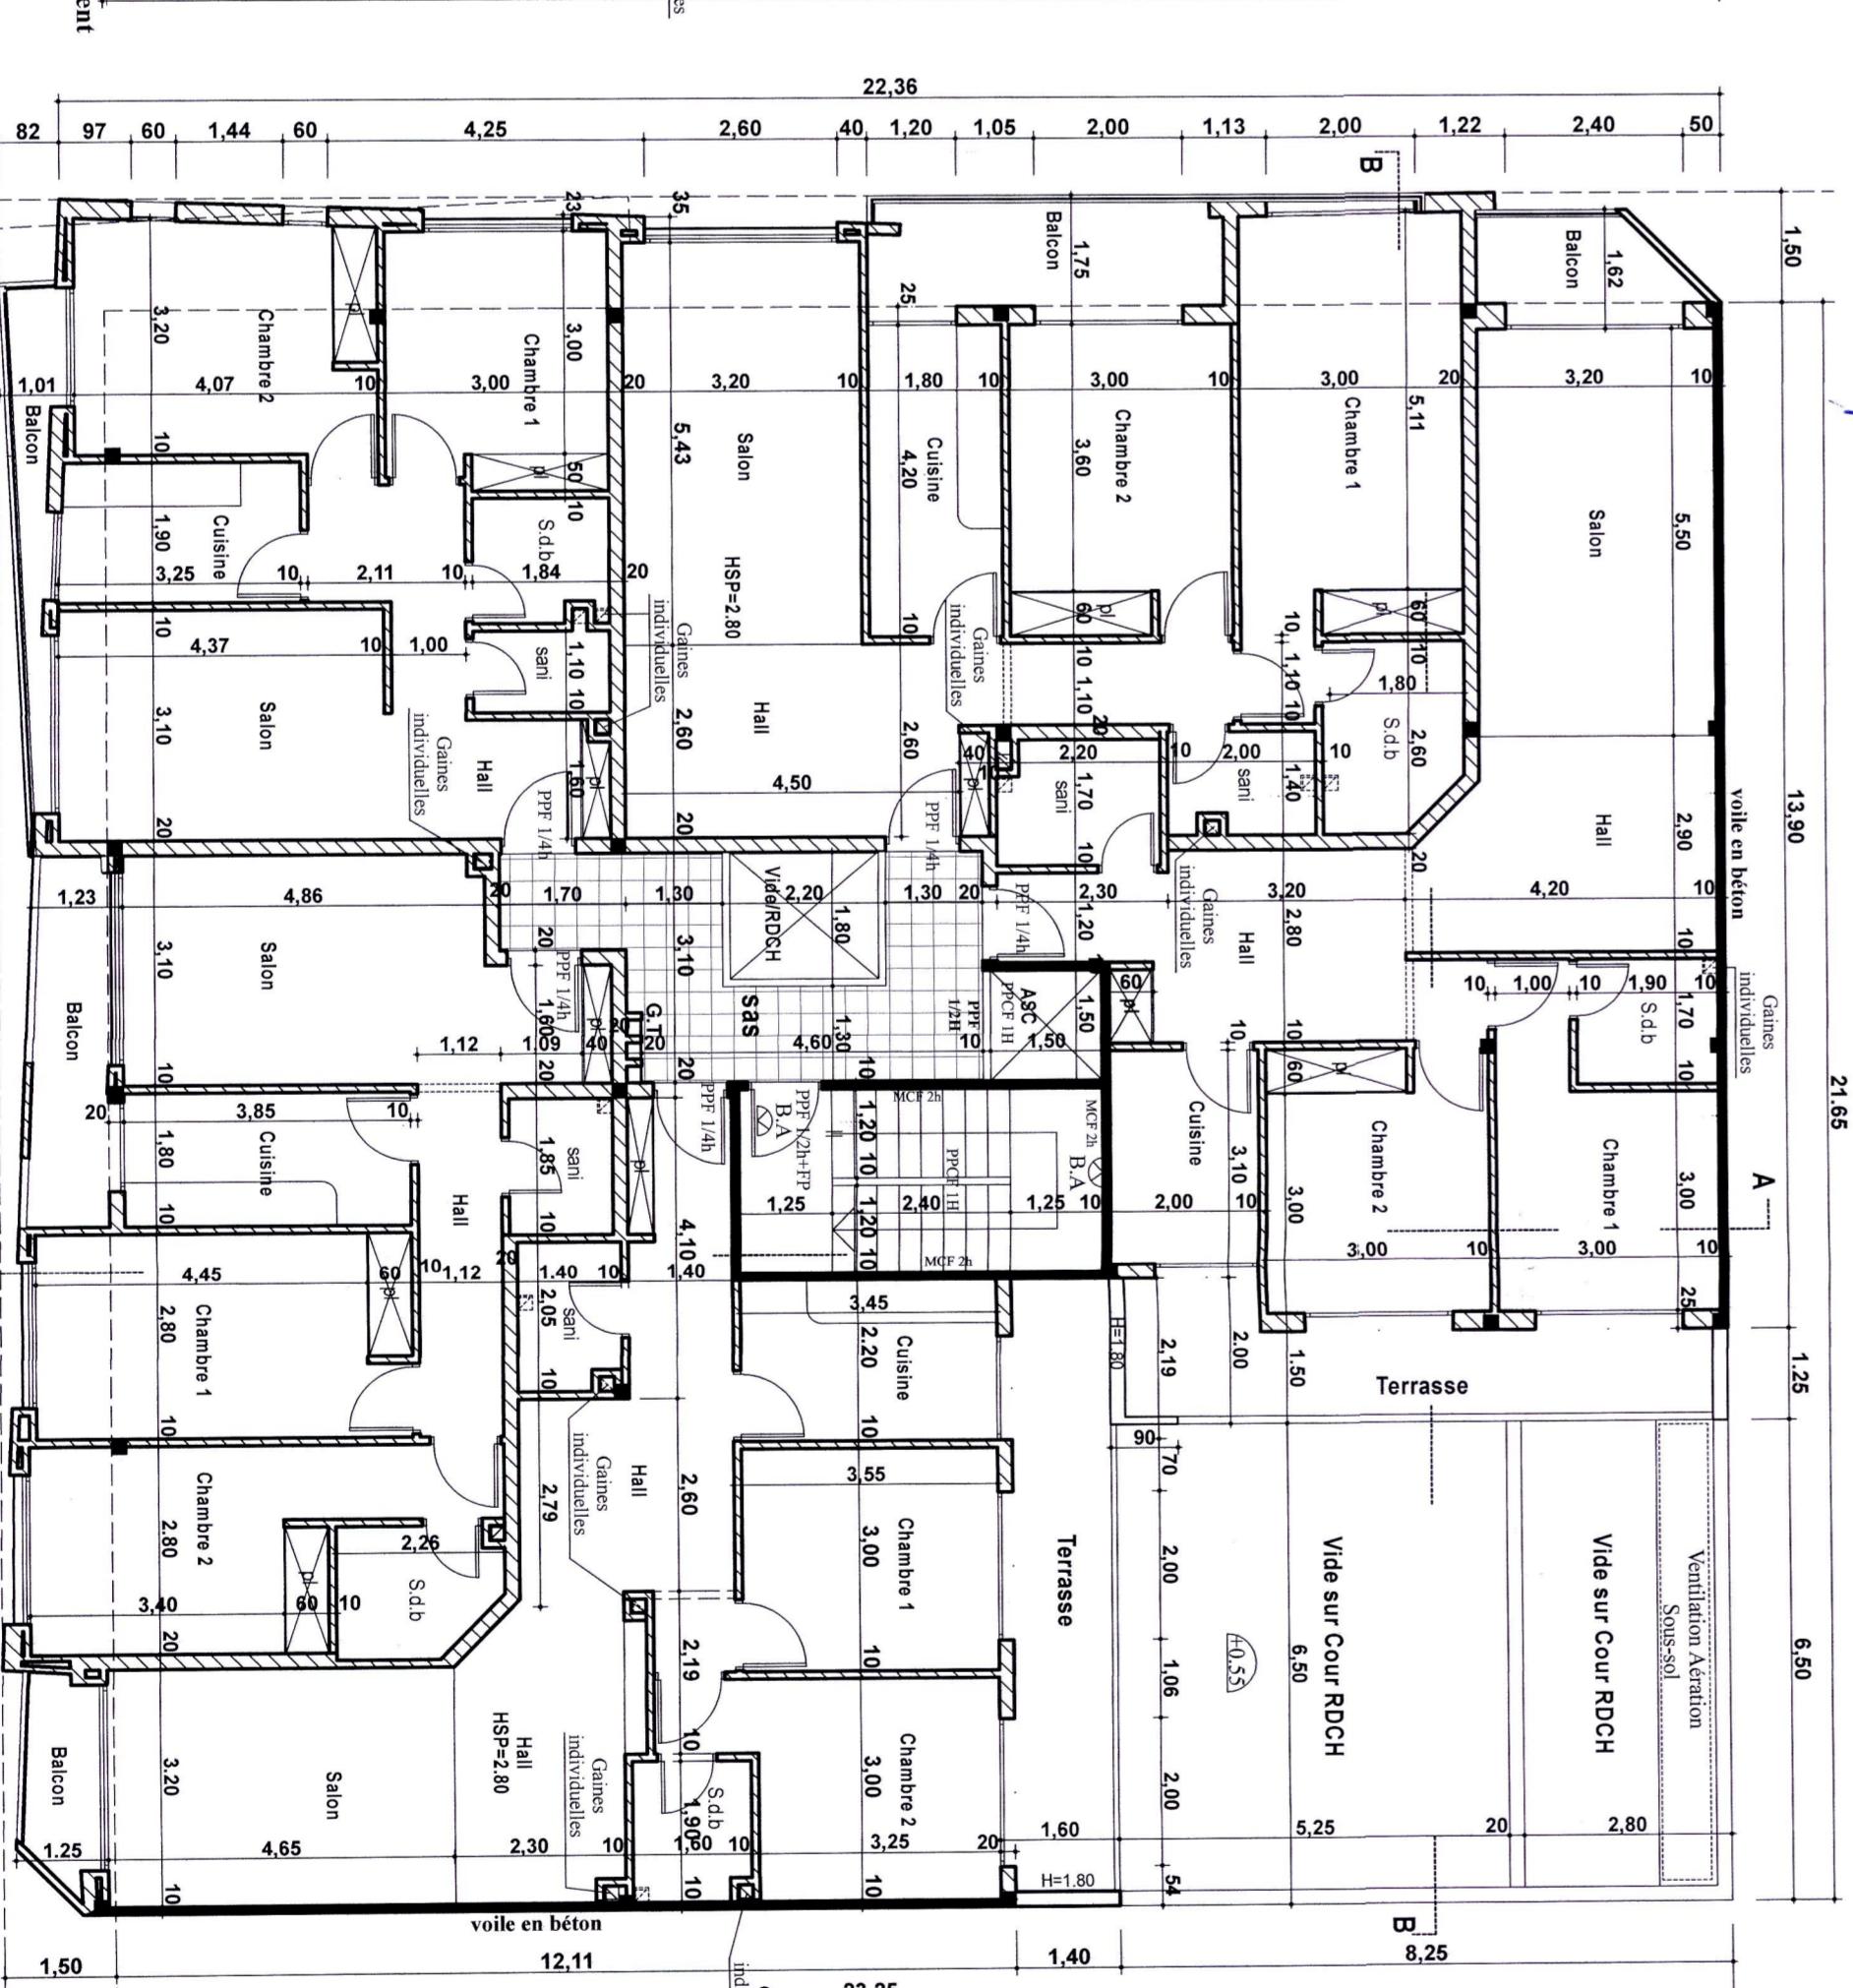

1er ETAGE

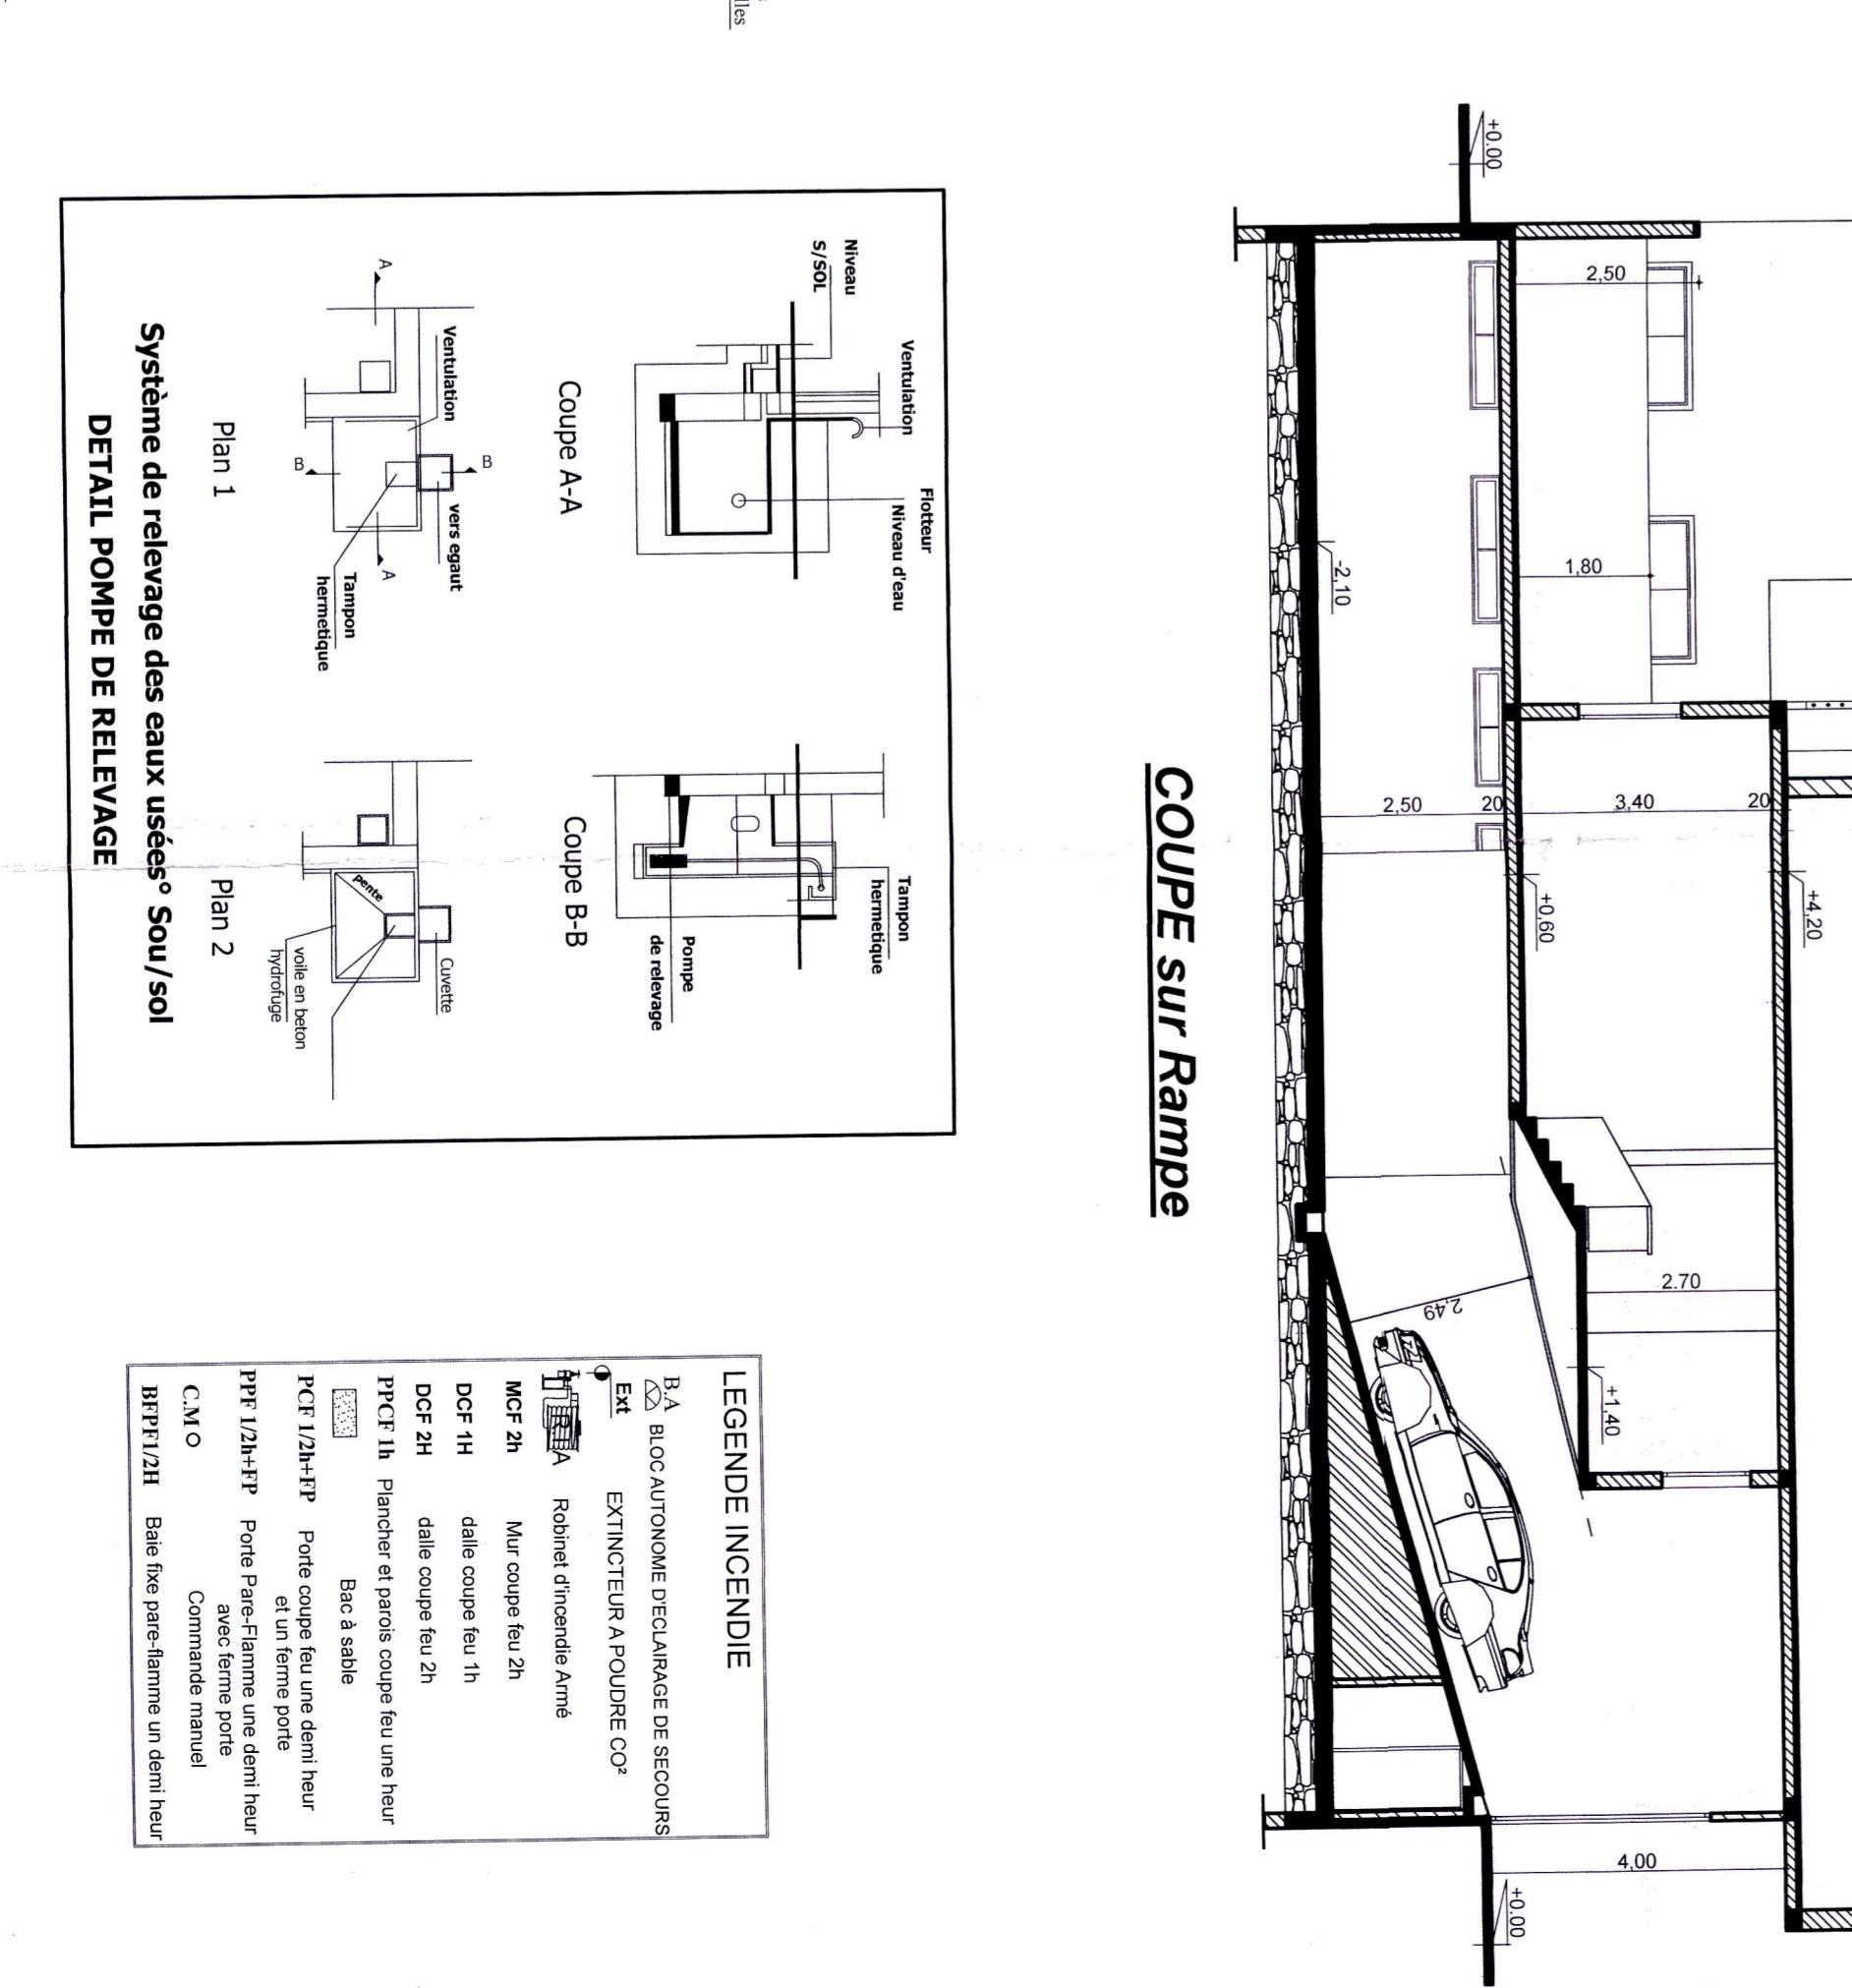

Système de relevage des eaux usées° Sou/sol

DETAIL POMPE DE RELEVAGE

Coupe A-A

Coupe B-B

LEGENDE INCENDIE

B.A	BLOC AUTONOME D'ALARME DE SECOURS
Ext	EXTINCTEUR A POUDRE CO ₂
	Robinet d'incendie Armé
MCF 2h	Mur coupe feu 2h
DCF 1H	dalle coupe feu 1h
DCF 2H	dalle coupe feu 2h
	Plancher et parois coupe feu une heure
PPCF 1h	Bac à sable
PCF 1/2h+FP	Porte coupe feu une demi heure et un ferme porte
PPF 1/2h+FP	Porte Pare-Flamme une demi heure avec ferme porte
C.M.O	Commande manuel
B.FPF1/2H	Baie fixe pare-flamme un demi heure

Plan 1

Plan 2

Ventilation

Niveau S/SOL

Flooteur Niveau d'eau

Tampon hermetique

Pompe de relevage

Coupe A-A

Coupe B-B


Ventilation vers égout

Tampon hermetique


Cuvette

pente


voile en béton hydrofuge

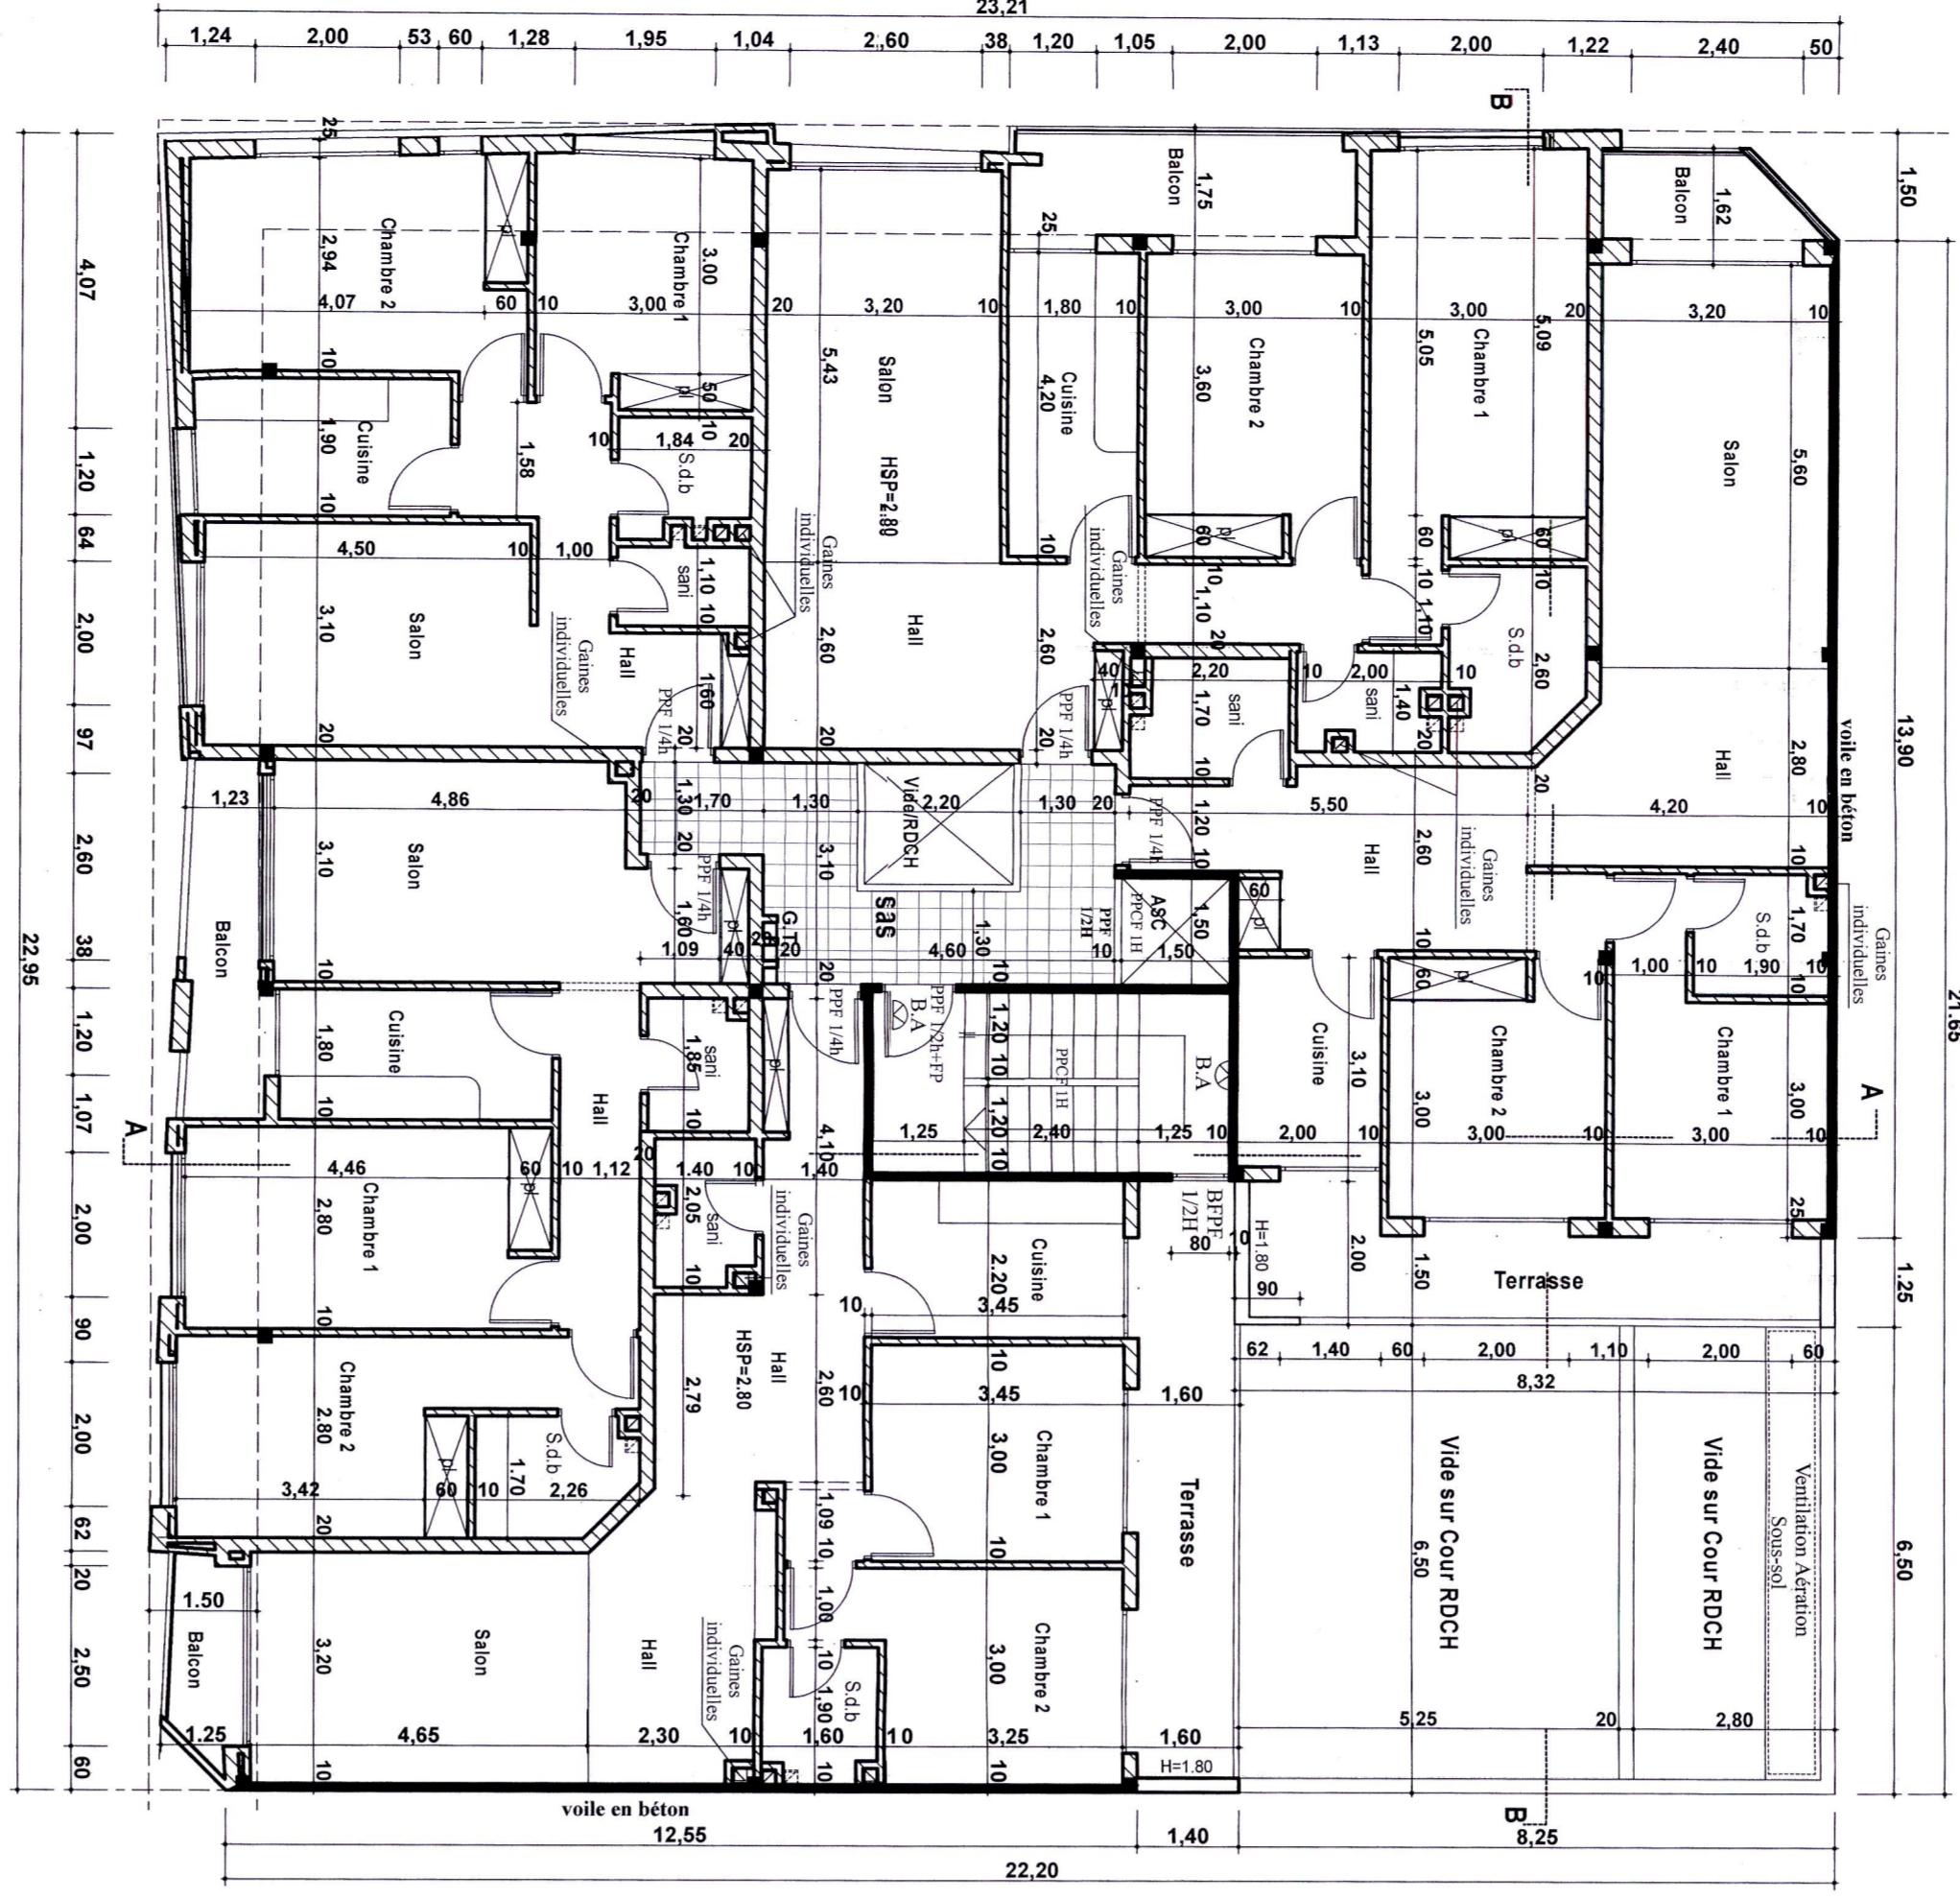


2eme ETAGE

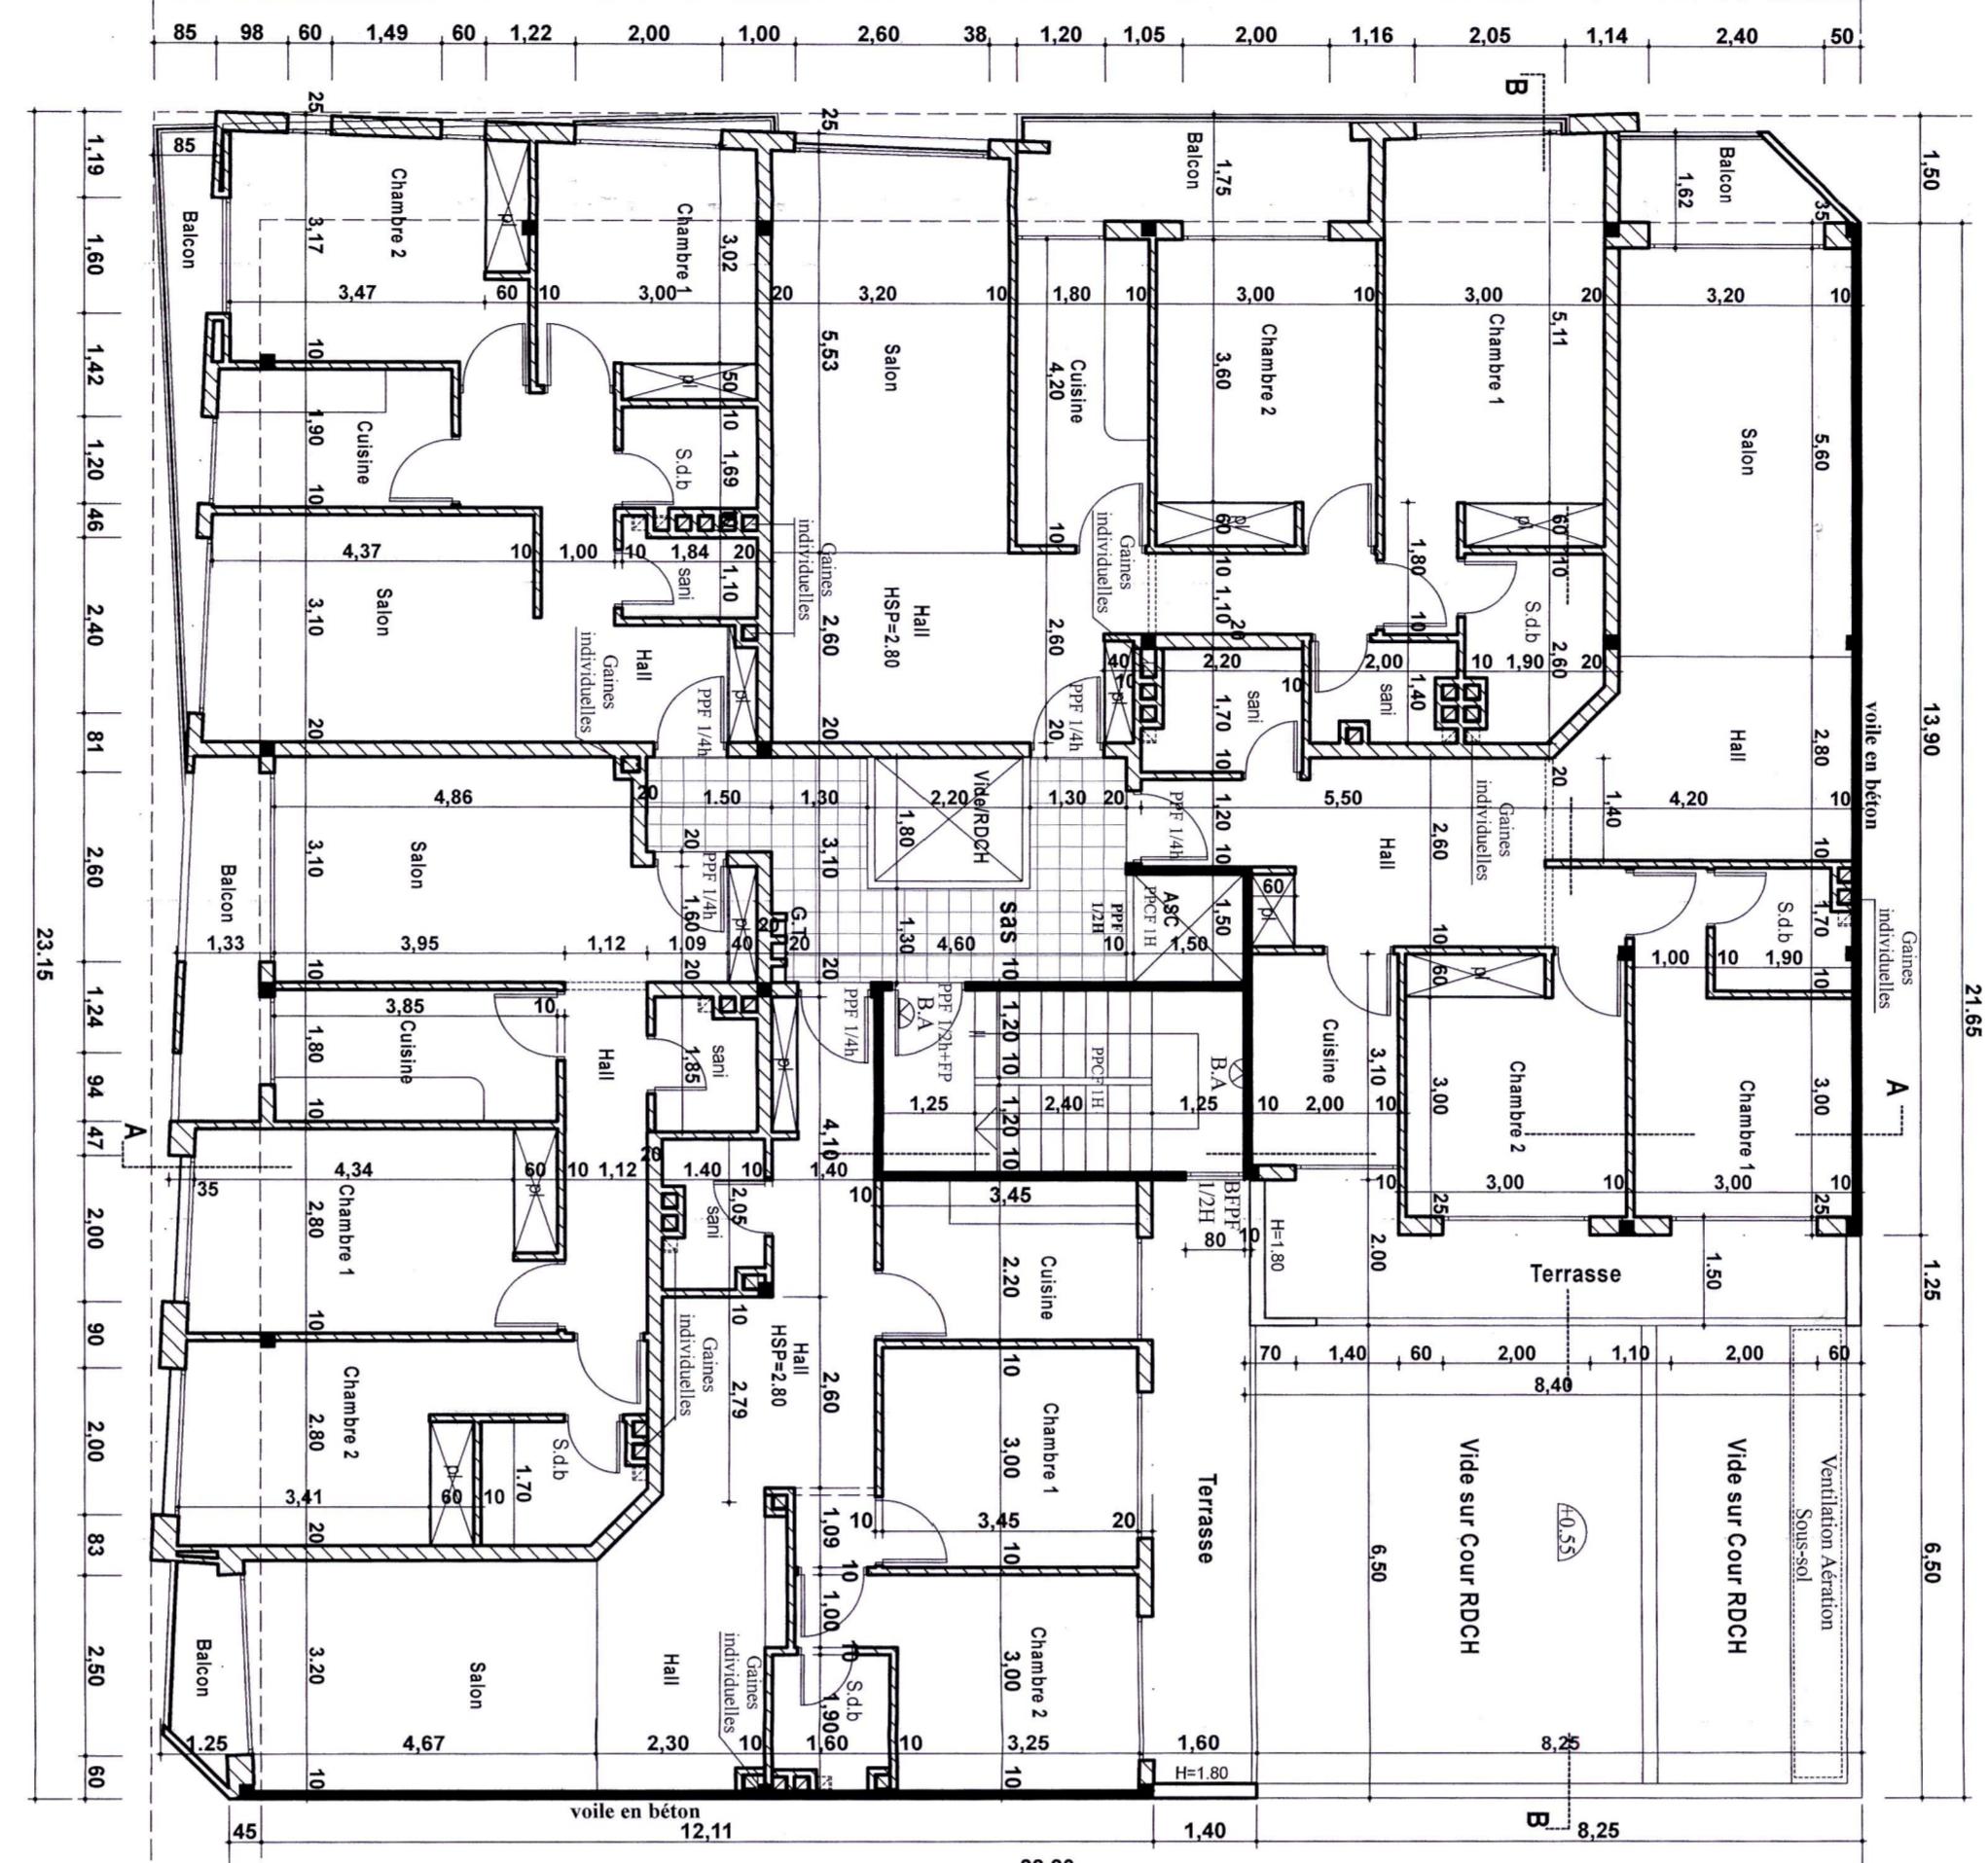

3 eme ETAGE

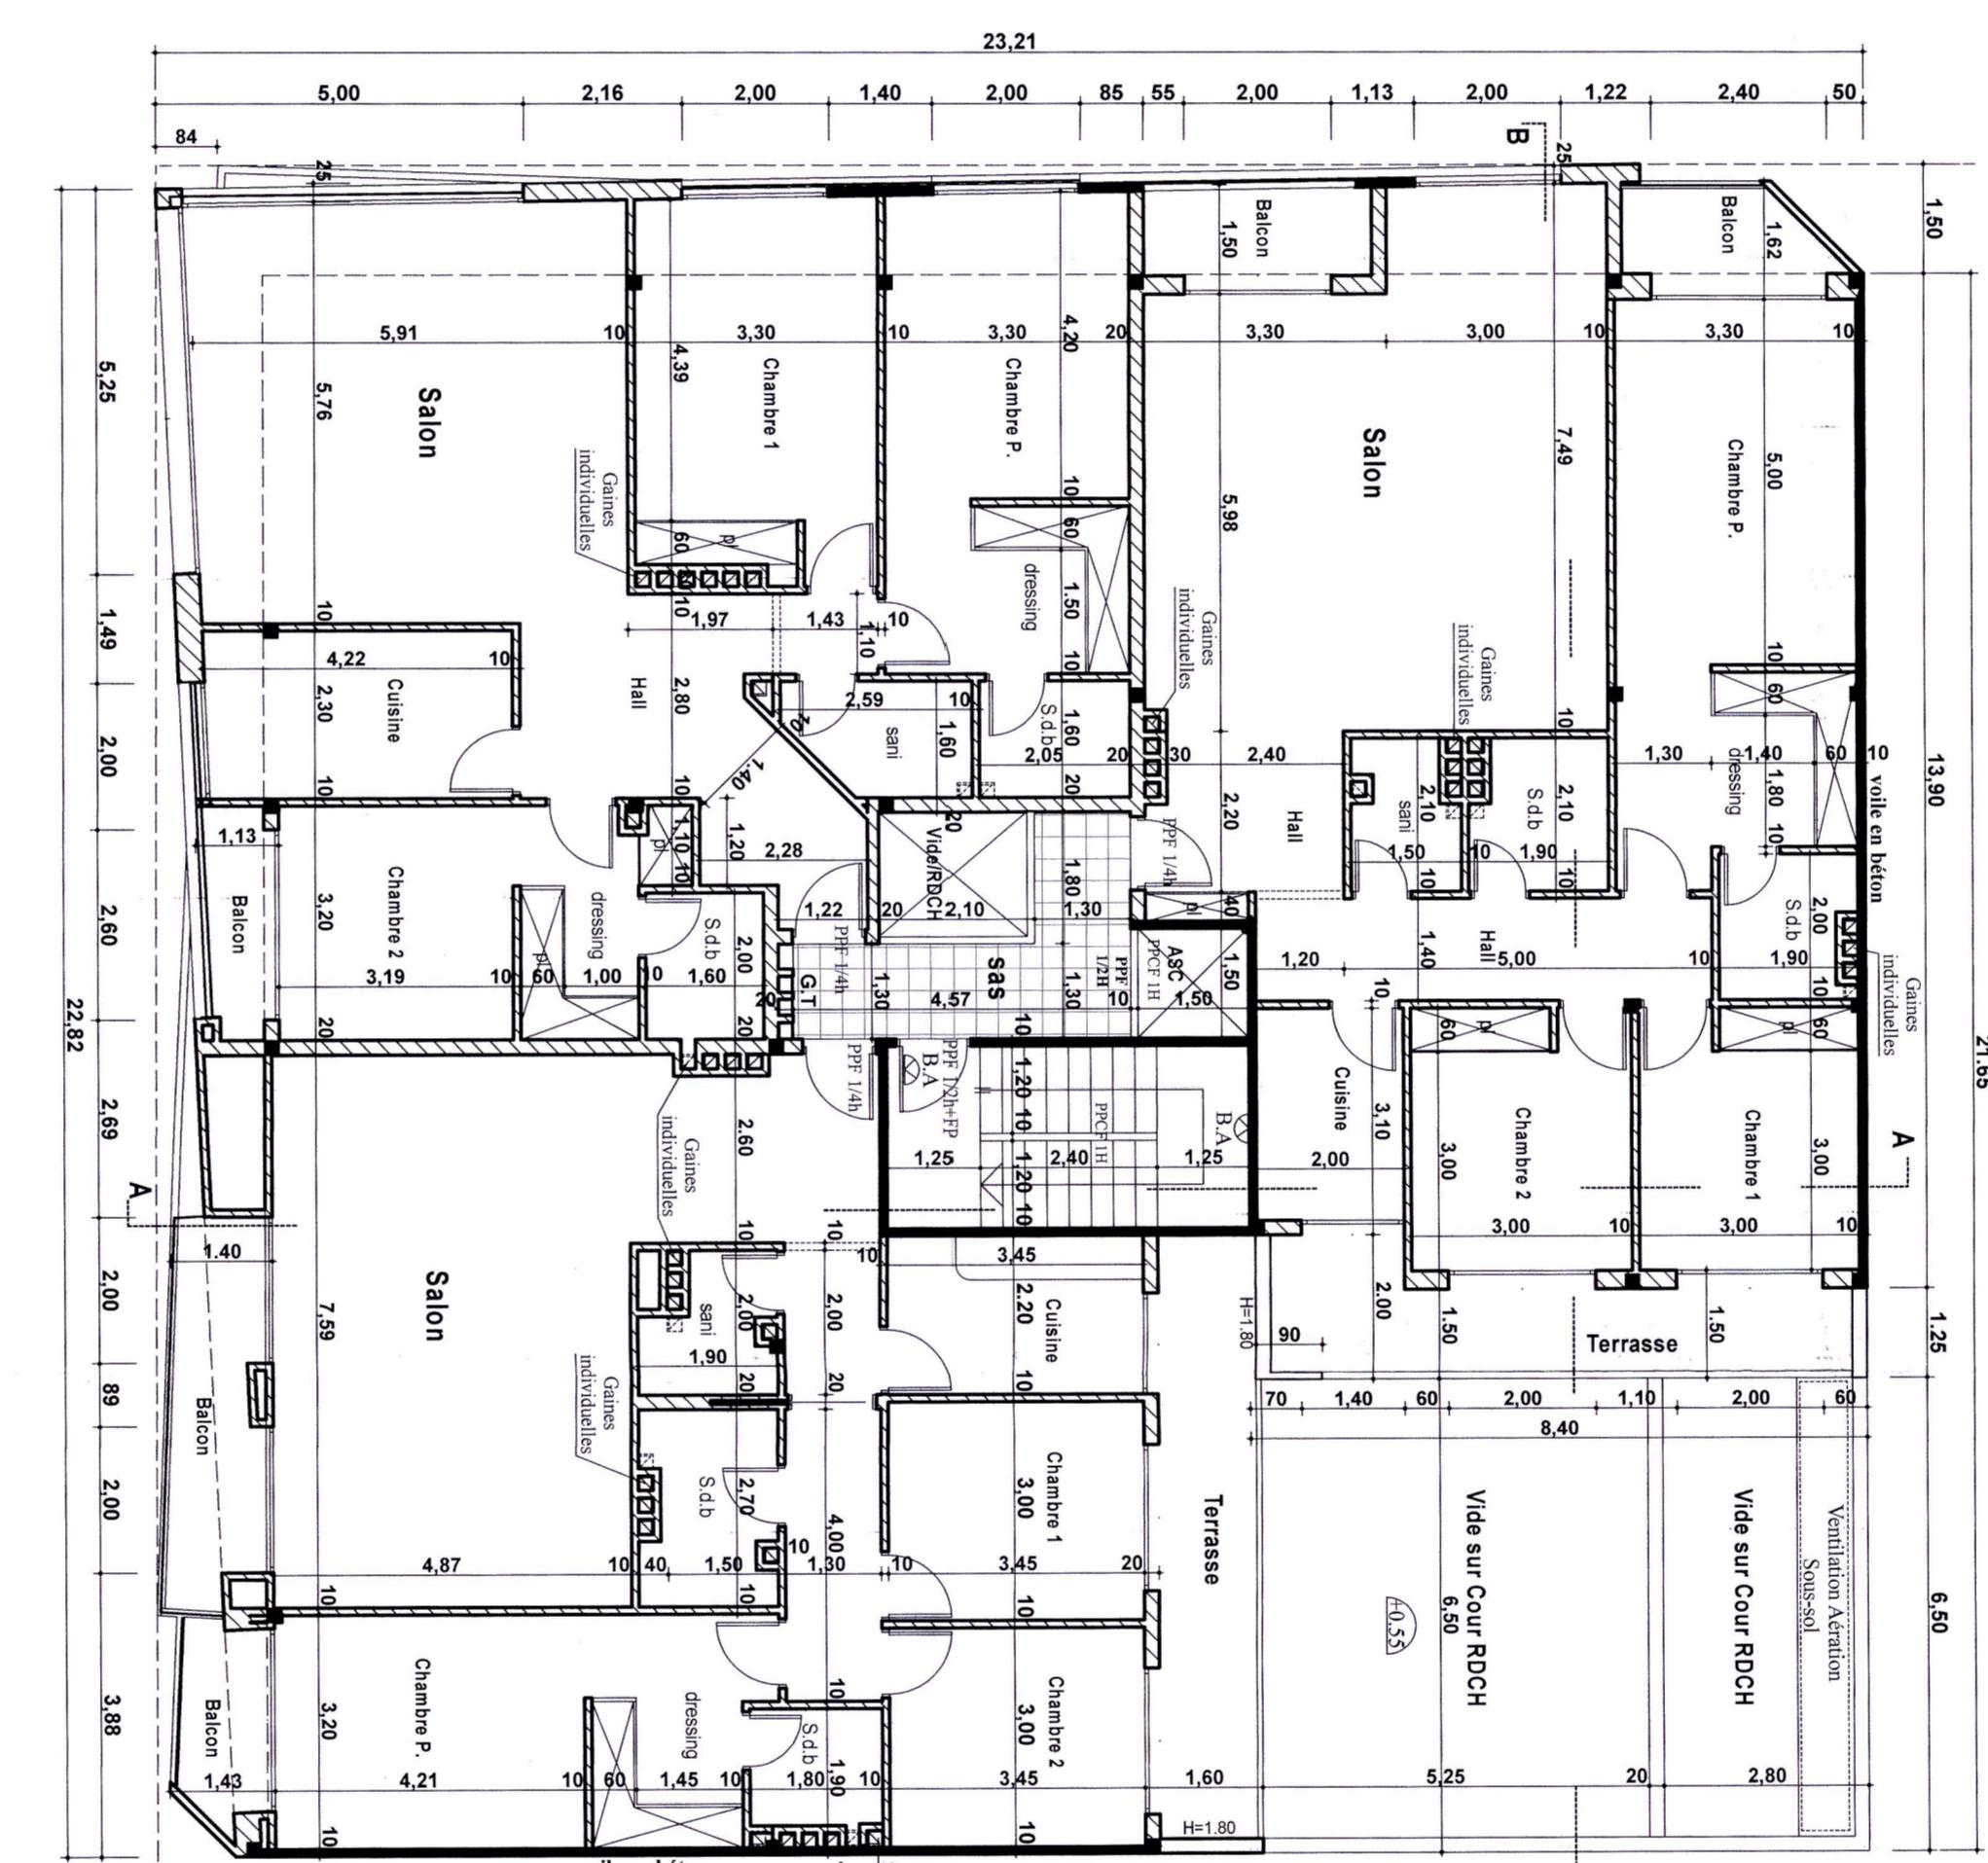


4eme ETAGE

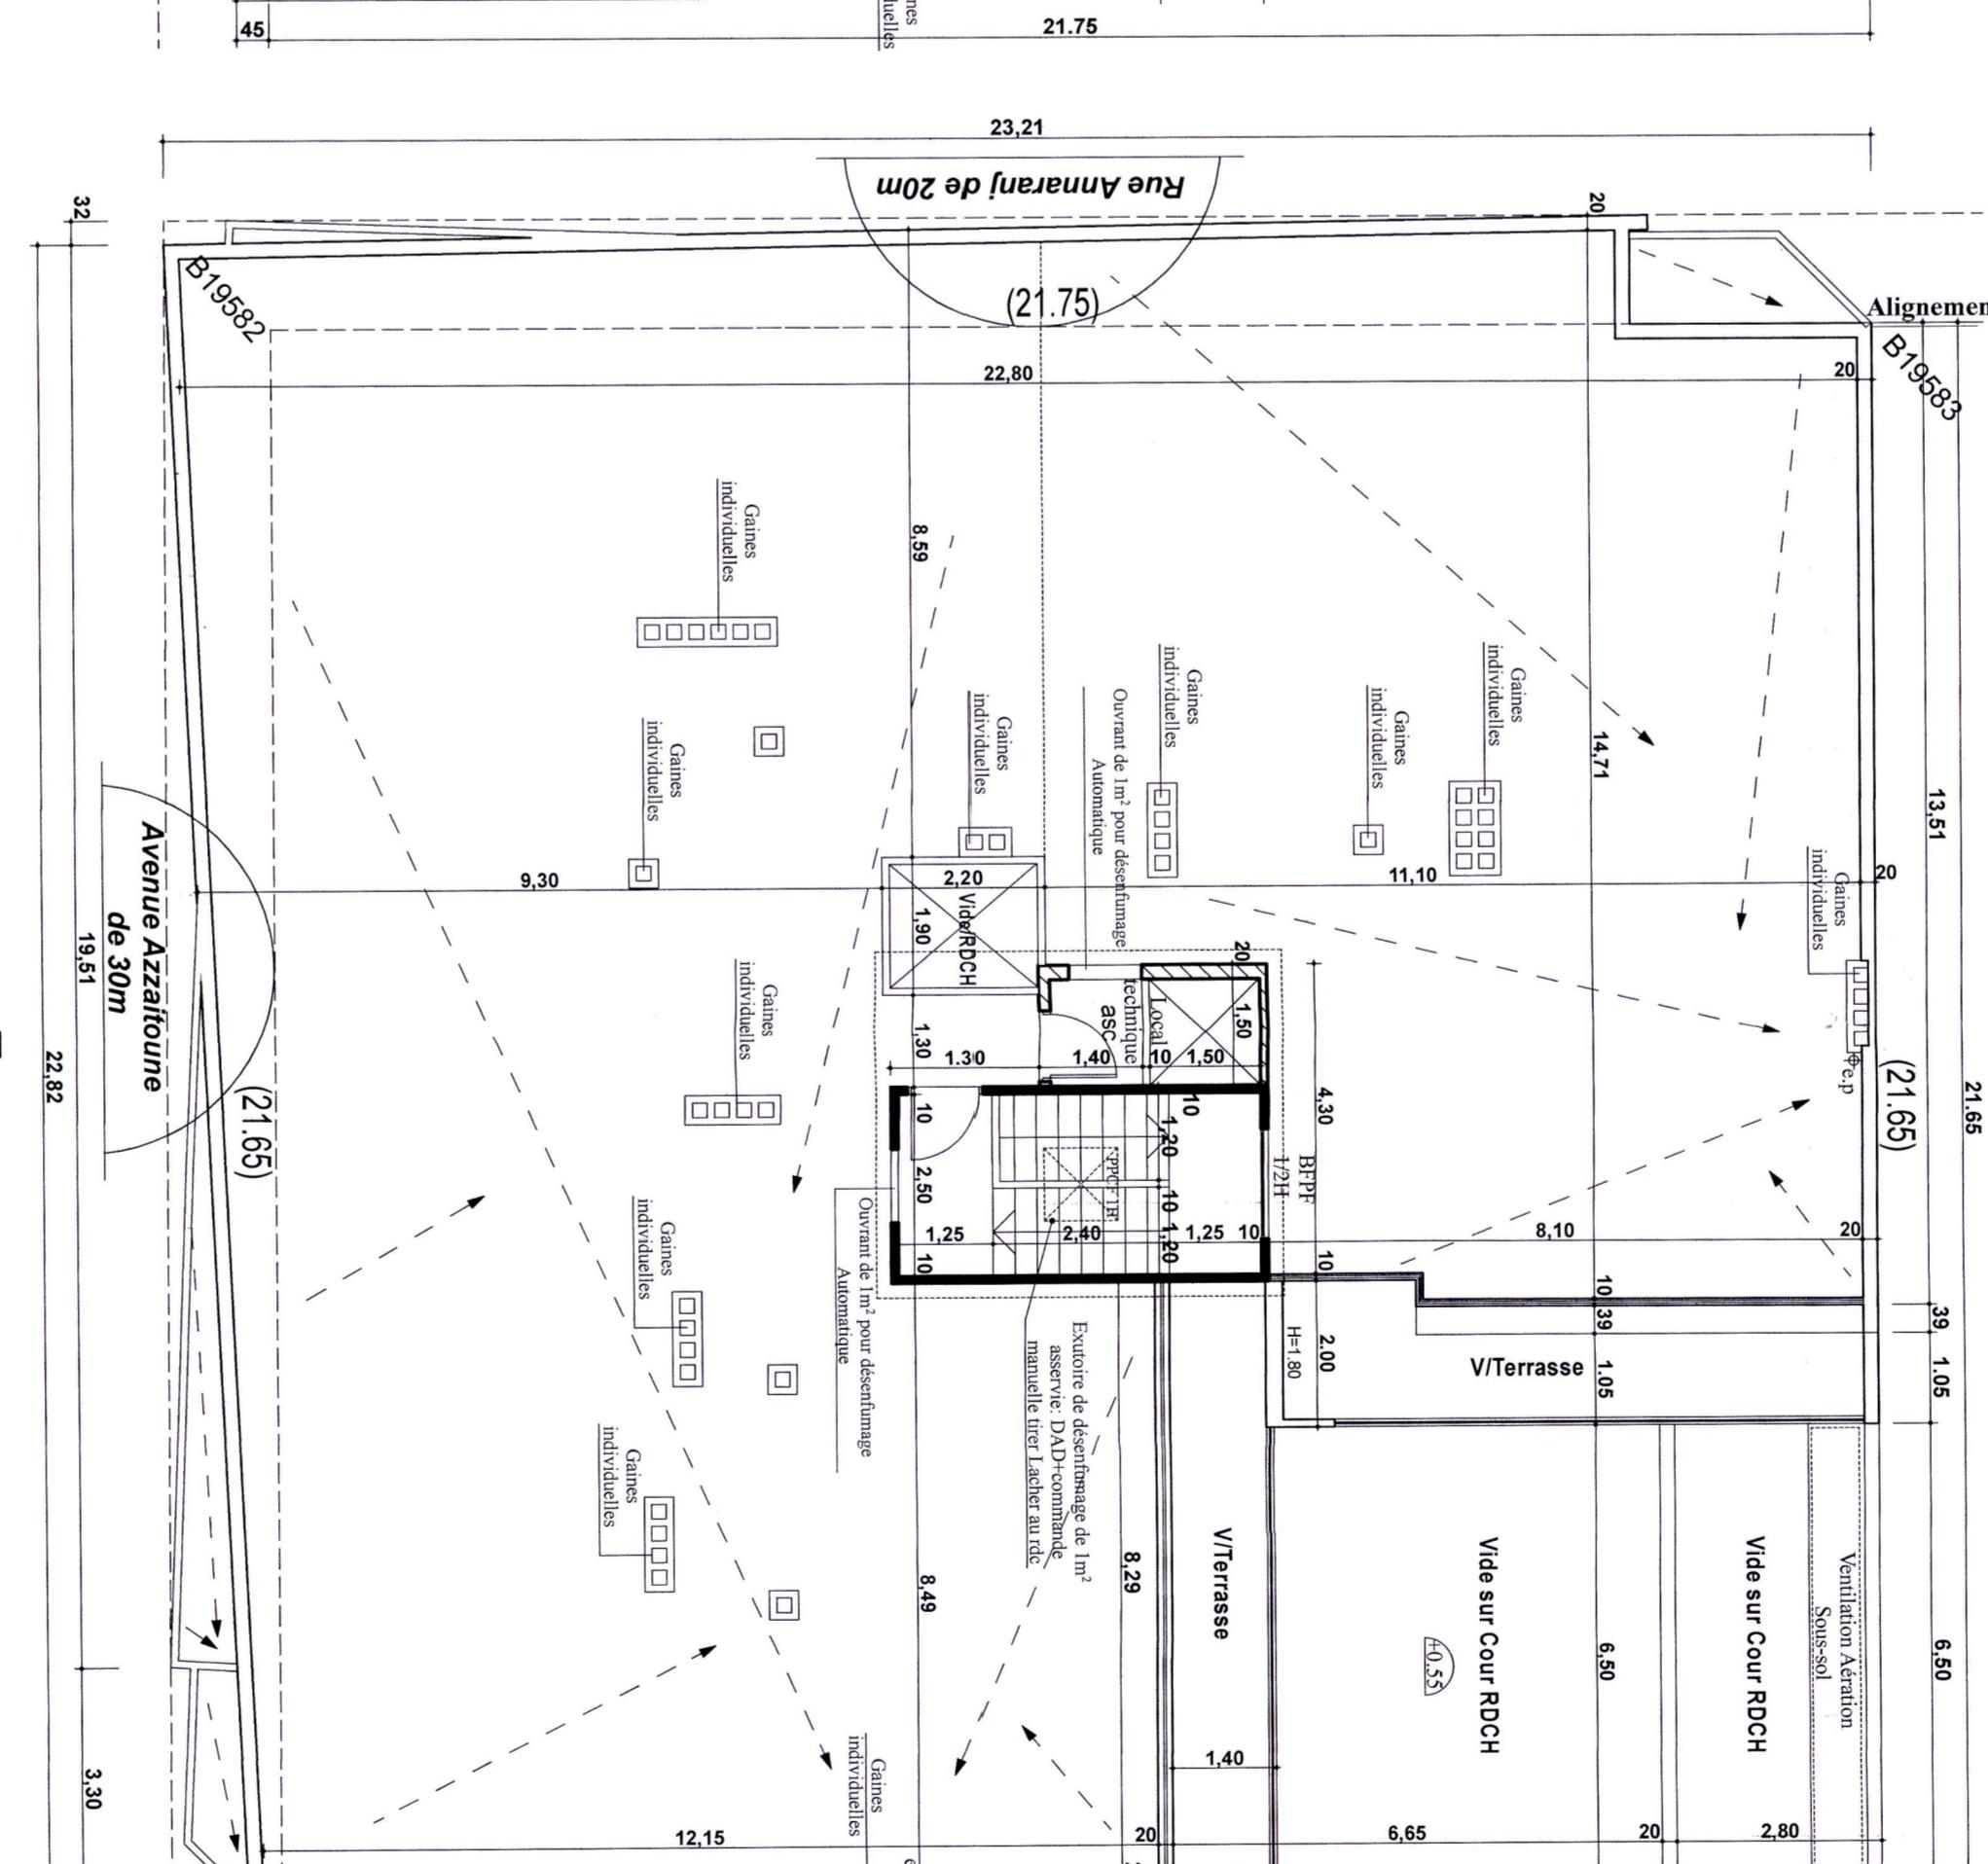


Terrasse



PLAN DE SITUATION

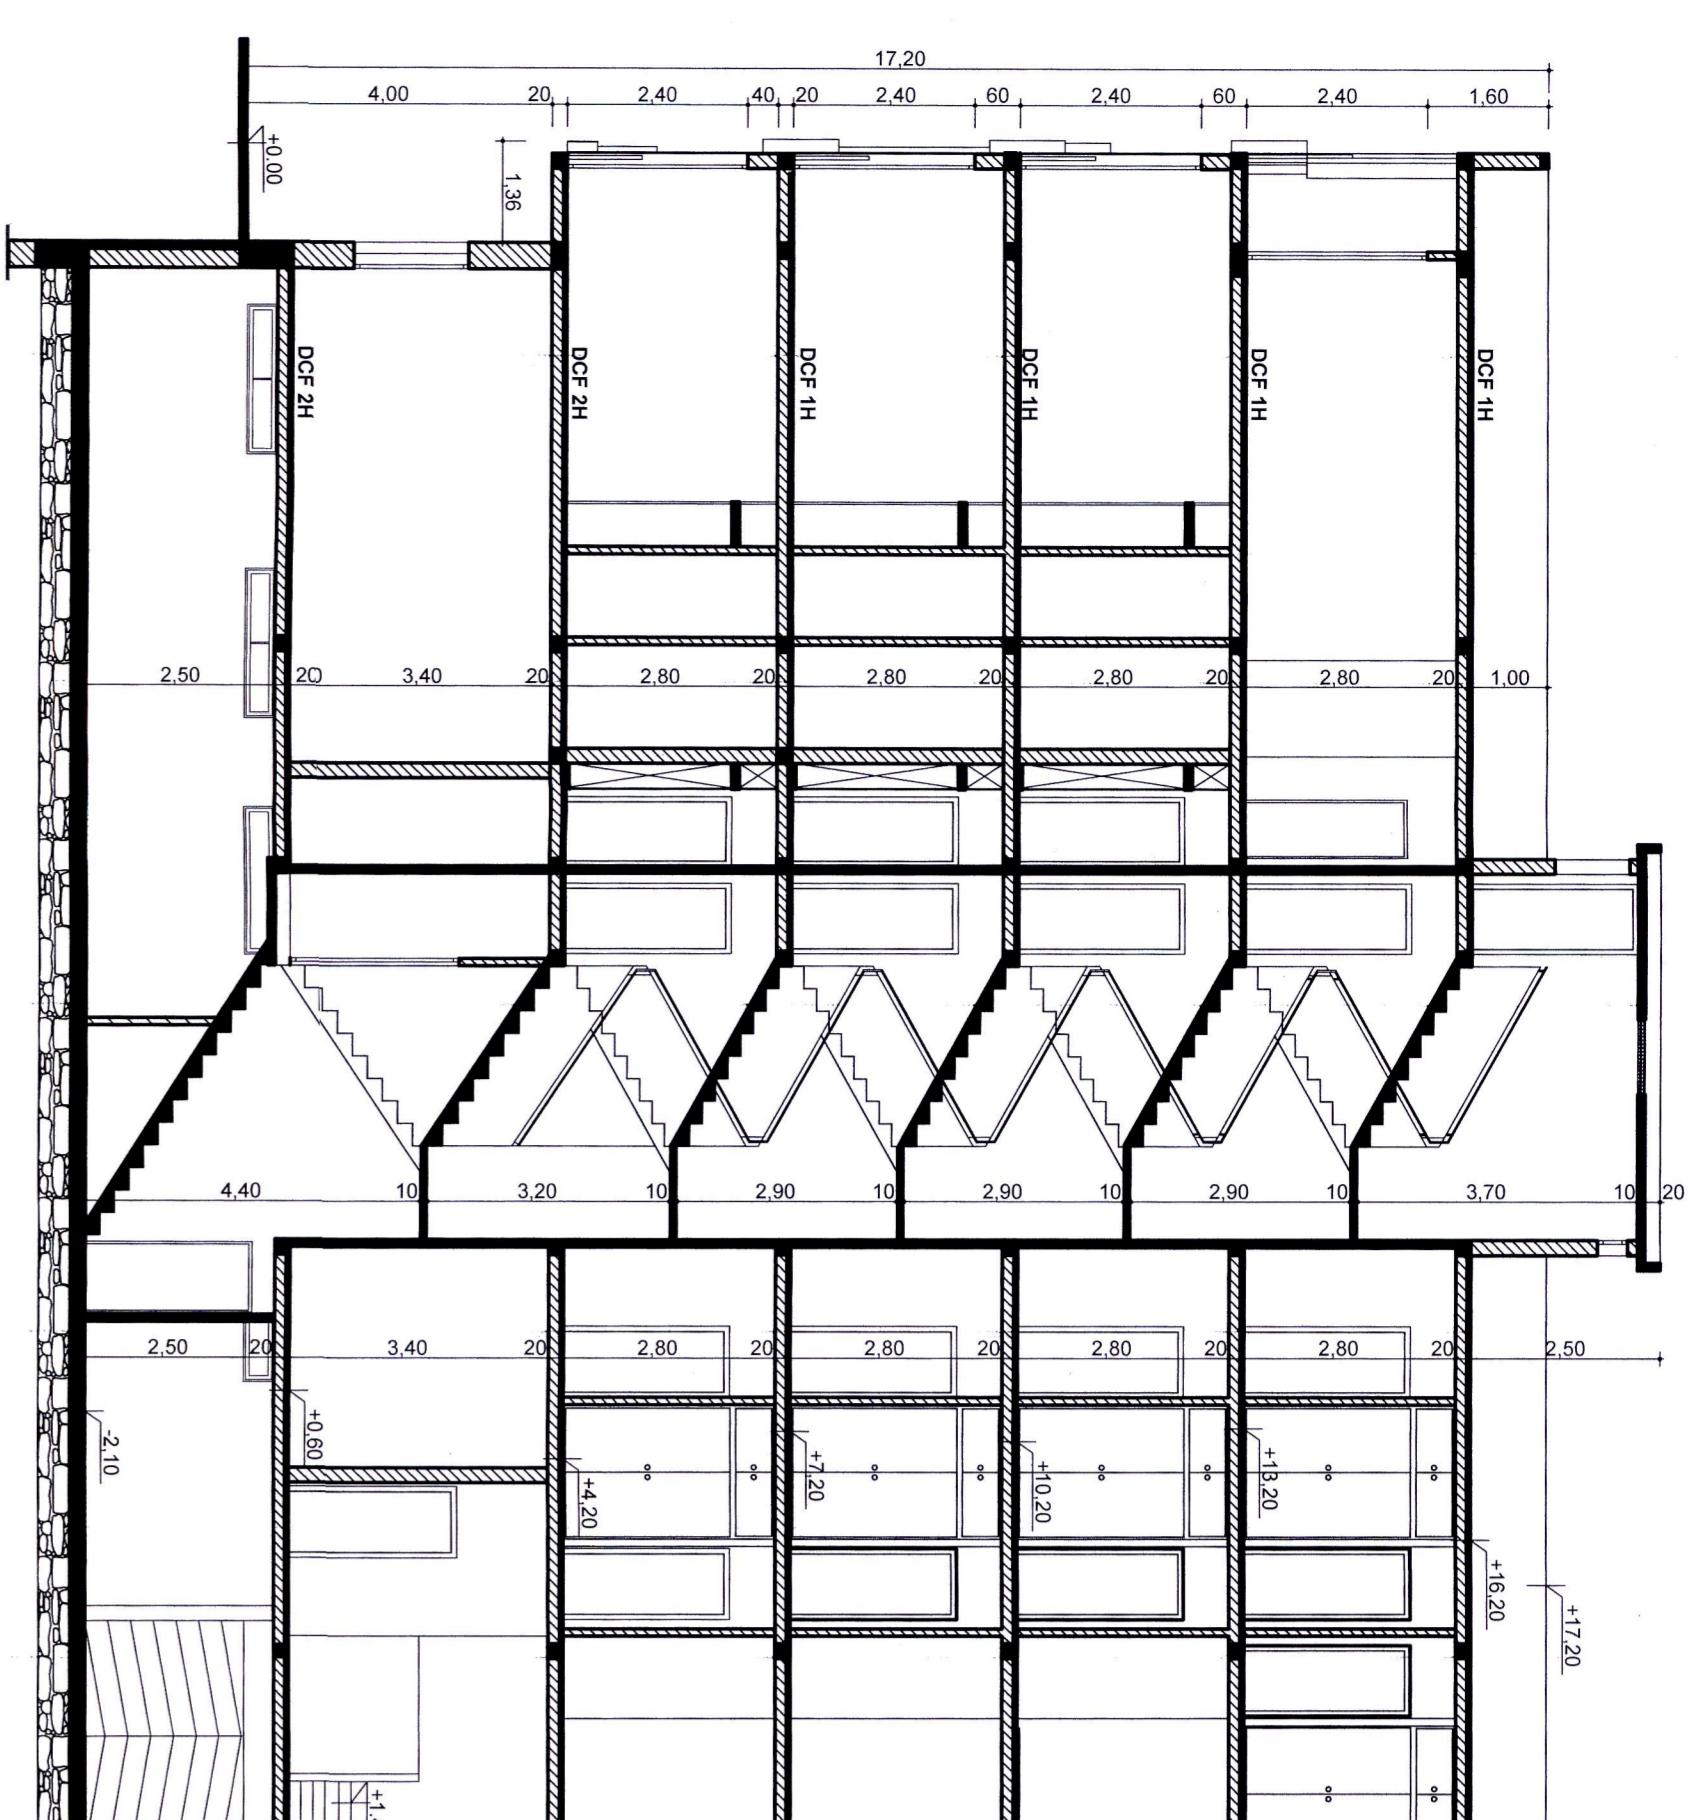

COUPE A-A

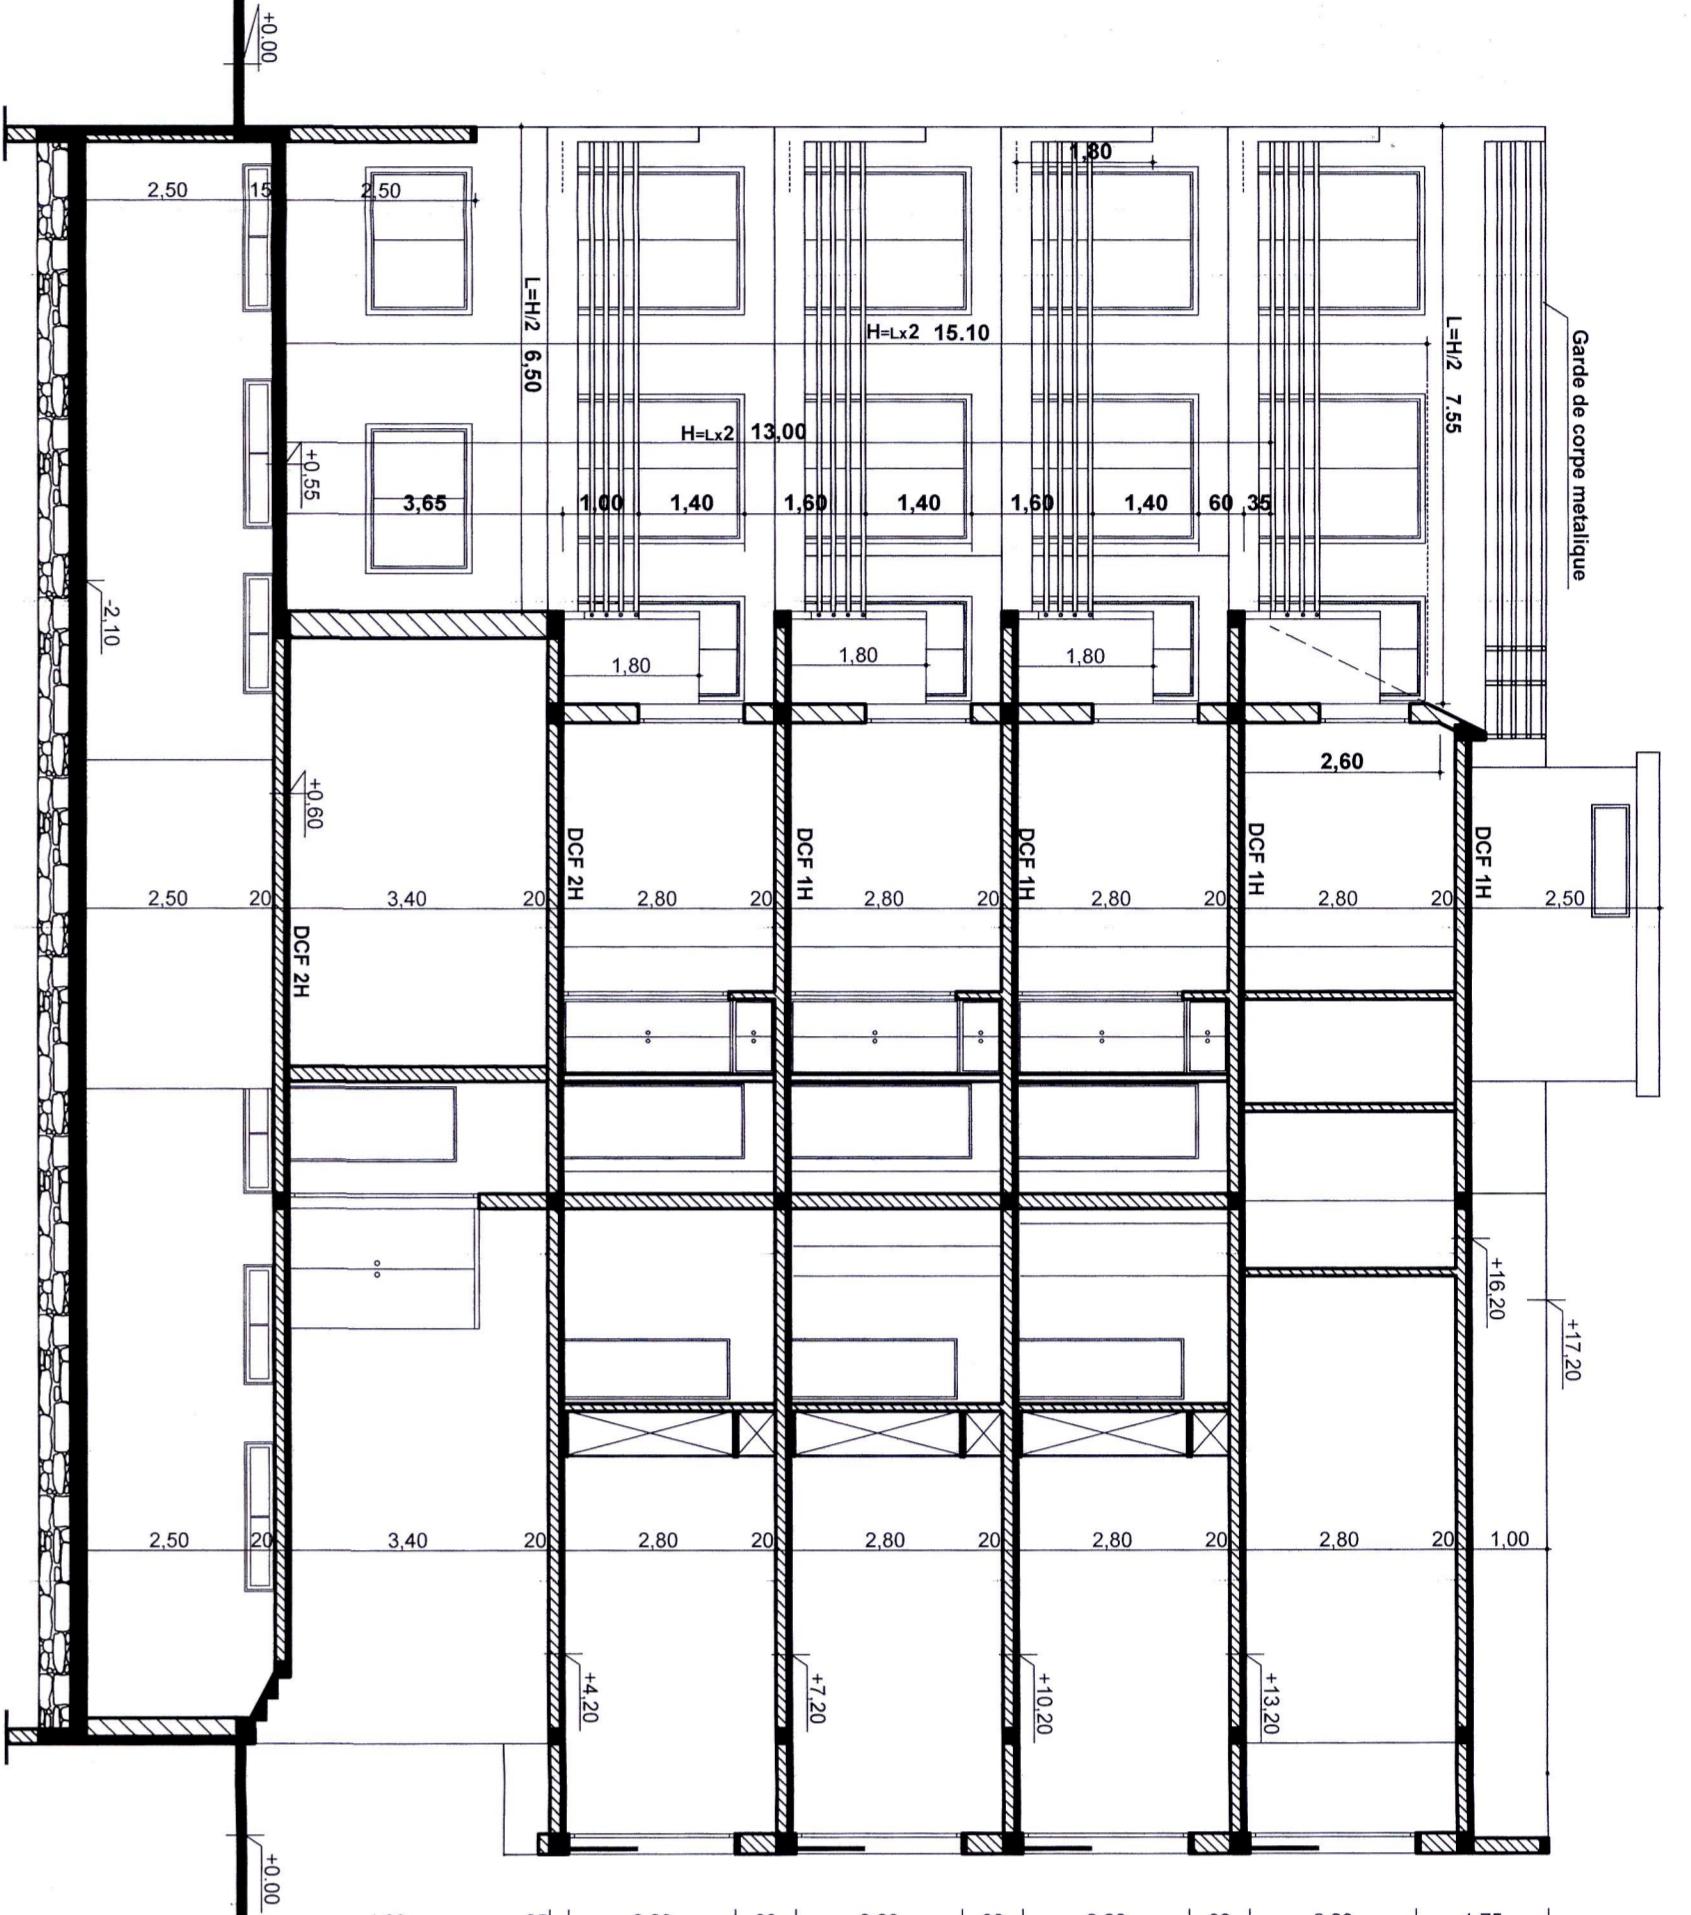

COUPE B-B

