


## Route Côtier

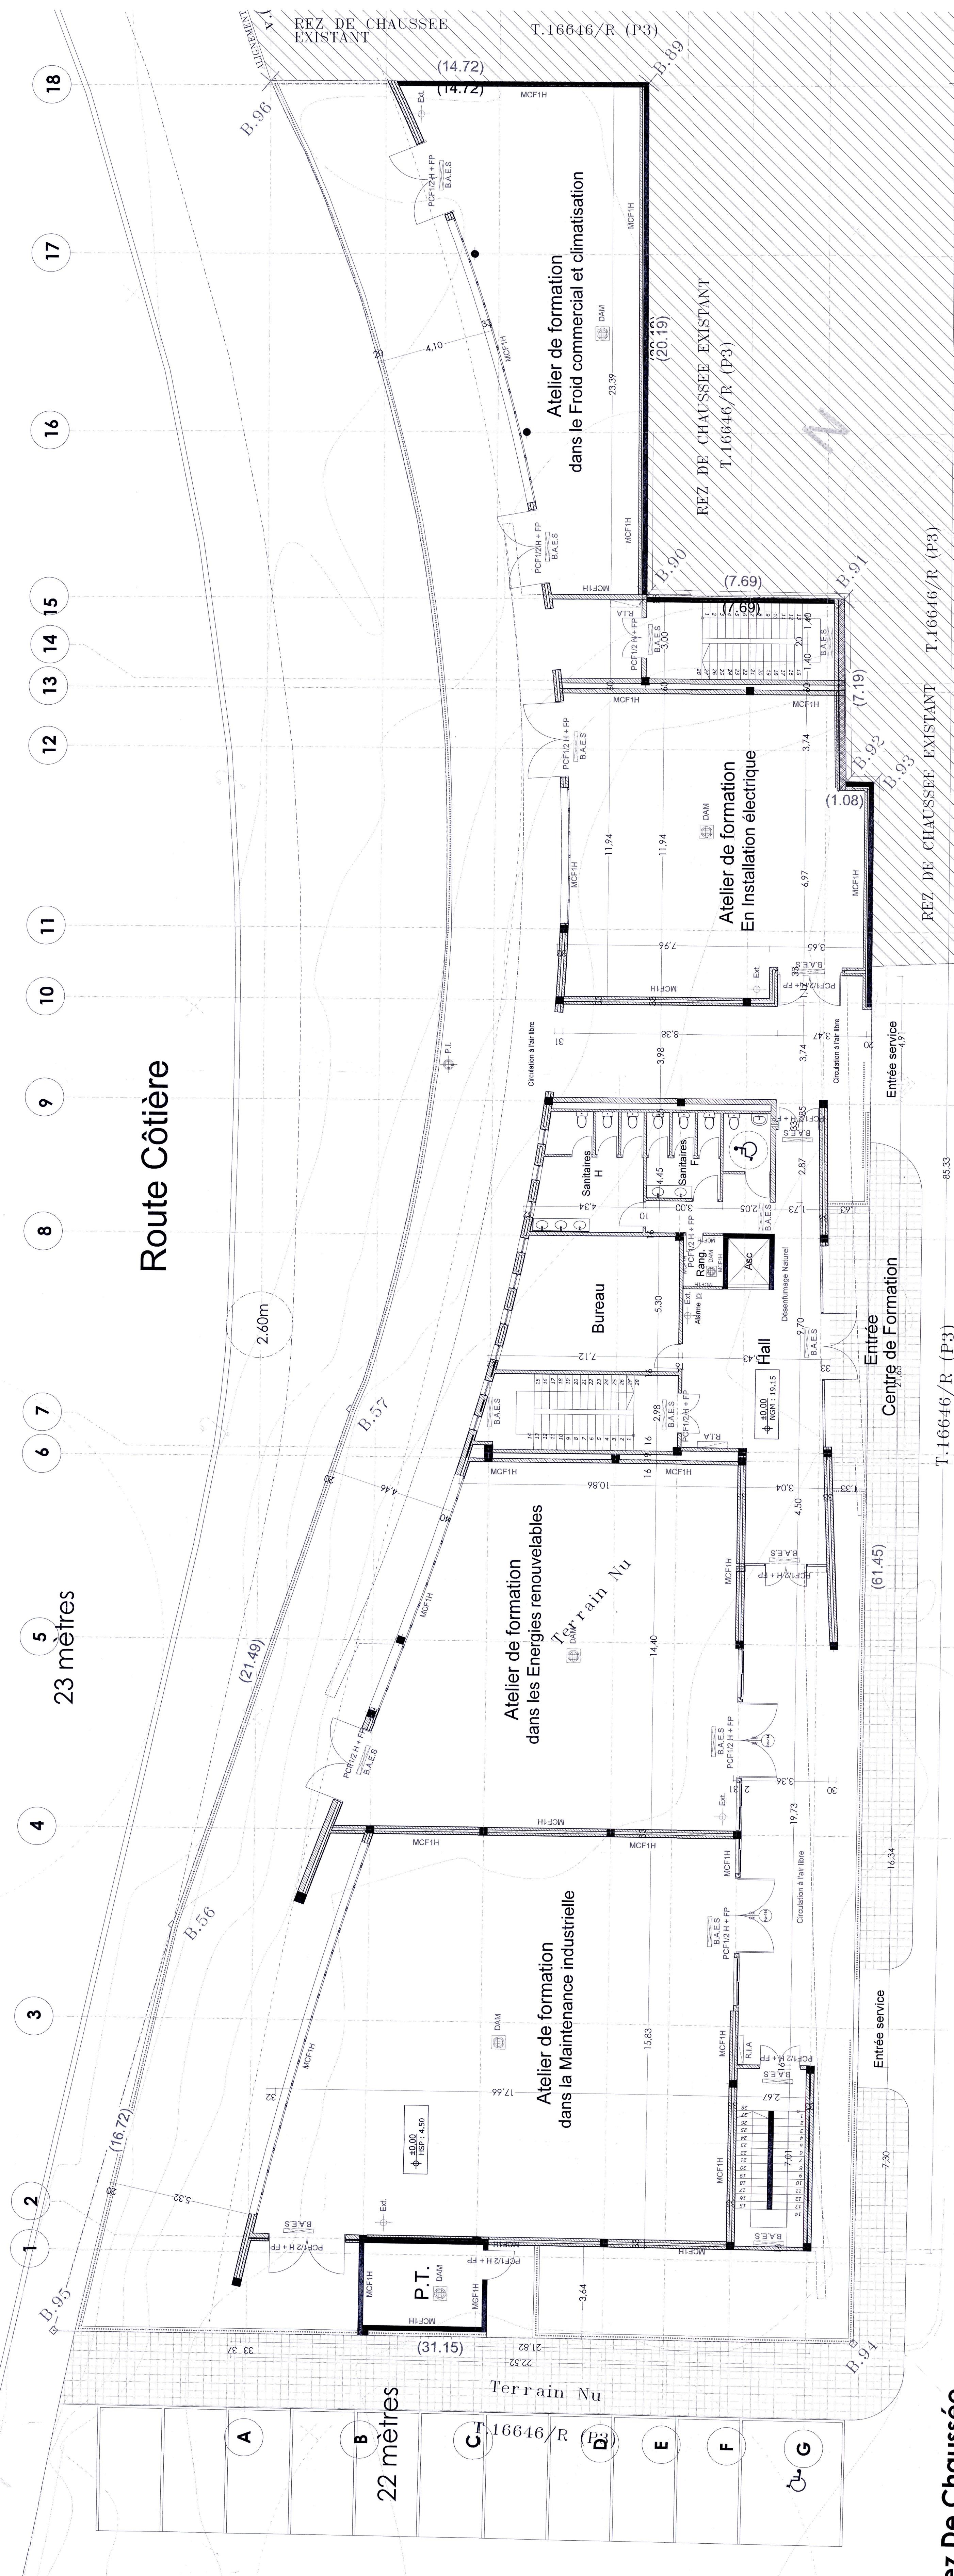

## Rez De Chaussée




## LEGENDE POMPIERS

|            |  |
|------------|--|
| PCF1H + FP | Porte coupe feu/porte à fermeture 12 heure + ferme porte |
| MCF/H      | Porte coupe feu 1 heure                                  |
| Ext.       | Extincteur à eau pulvrisseur 6L                          |
| B.A.E.S    | Barre autonome d'éclairage de sécurité                   |
| DAM        | Interruption automatique en cas de panne                 |
| R.I.A.     | Robot d'incendie armé sur tambour mobile                 |
| P.L.       | Poteau d'incendie  |
| ALARME     | Alarme   |
| DN         | Déclencheur asservi à la détection automatique           |

**ROYAUME DU MAROC**  
WILAYA DE LA REGION RABAT-SALE-KENITRA  
PREFECTURE DE RABAT  
COMMUNE DE HASAN

**MAÎTRE D'OUVRAGE:**  
FONDATION MOHAMMED V POUR LA SOLIDARITE

**PROJET DE CONSTRUCTION DU**  
**CENTRE DE FORMATION DANS LES MÉTIERS DE LA MAINTENANCE**  
**ET DES ÉNERGIES RENOUVELABLES À AKKARI - RABAT**

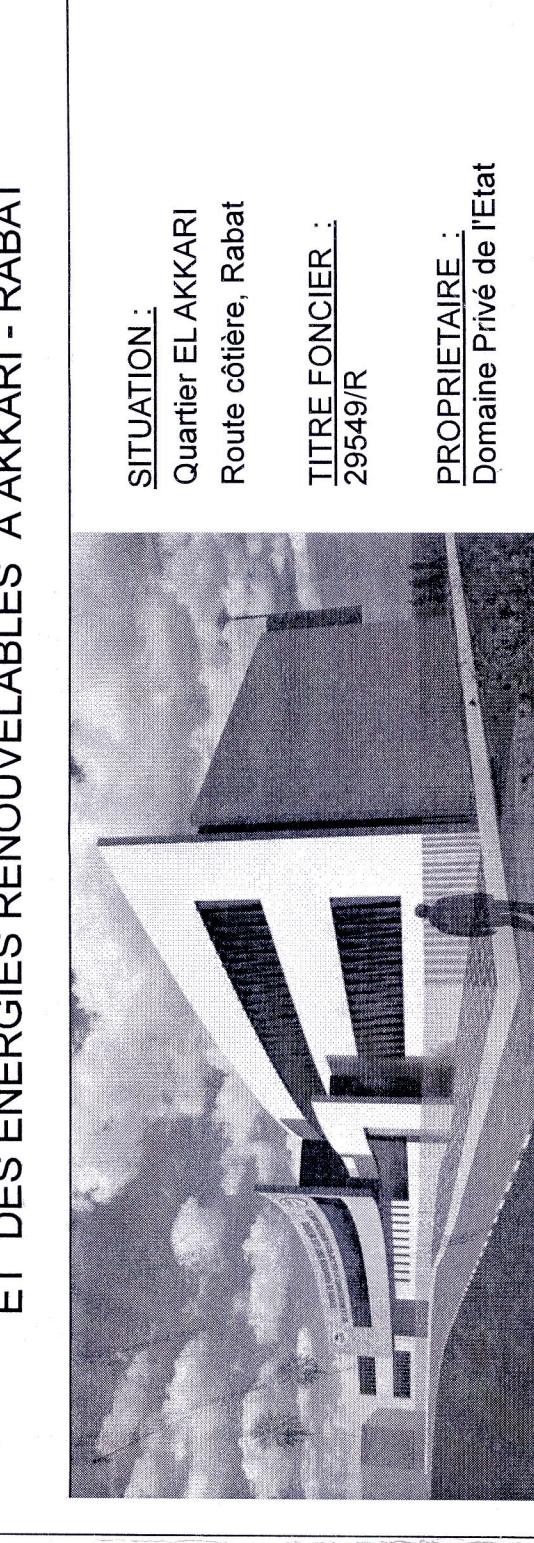

**GROUPEMENT D'ARCHITECTES**  
EL HADDOUKI MOUSTAKIM ARCHITECTE  
ATELIER CHARAF EL AYANI  
ATELIER CHAMIA ETAGNINI  
Dossier d'autorisation :  
Plan Rez de chaussée  
Plan 1er étage

**VISA**  
EL FAJJA, EL KHALIFI, EL HADDOUKI,  
EL HADDOUKI MOUSTAKIM, EL AYANI,  
ATELIER CHAMIA ETAGNINI  
Date : 28/01/2019

**Projet** 16CFA **Emetteur** ACE **Phase** DAC **Indice** D **Date** 28/01/2019 **Planche** 1/12